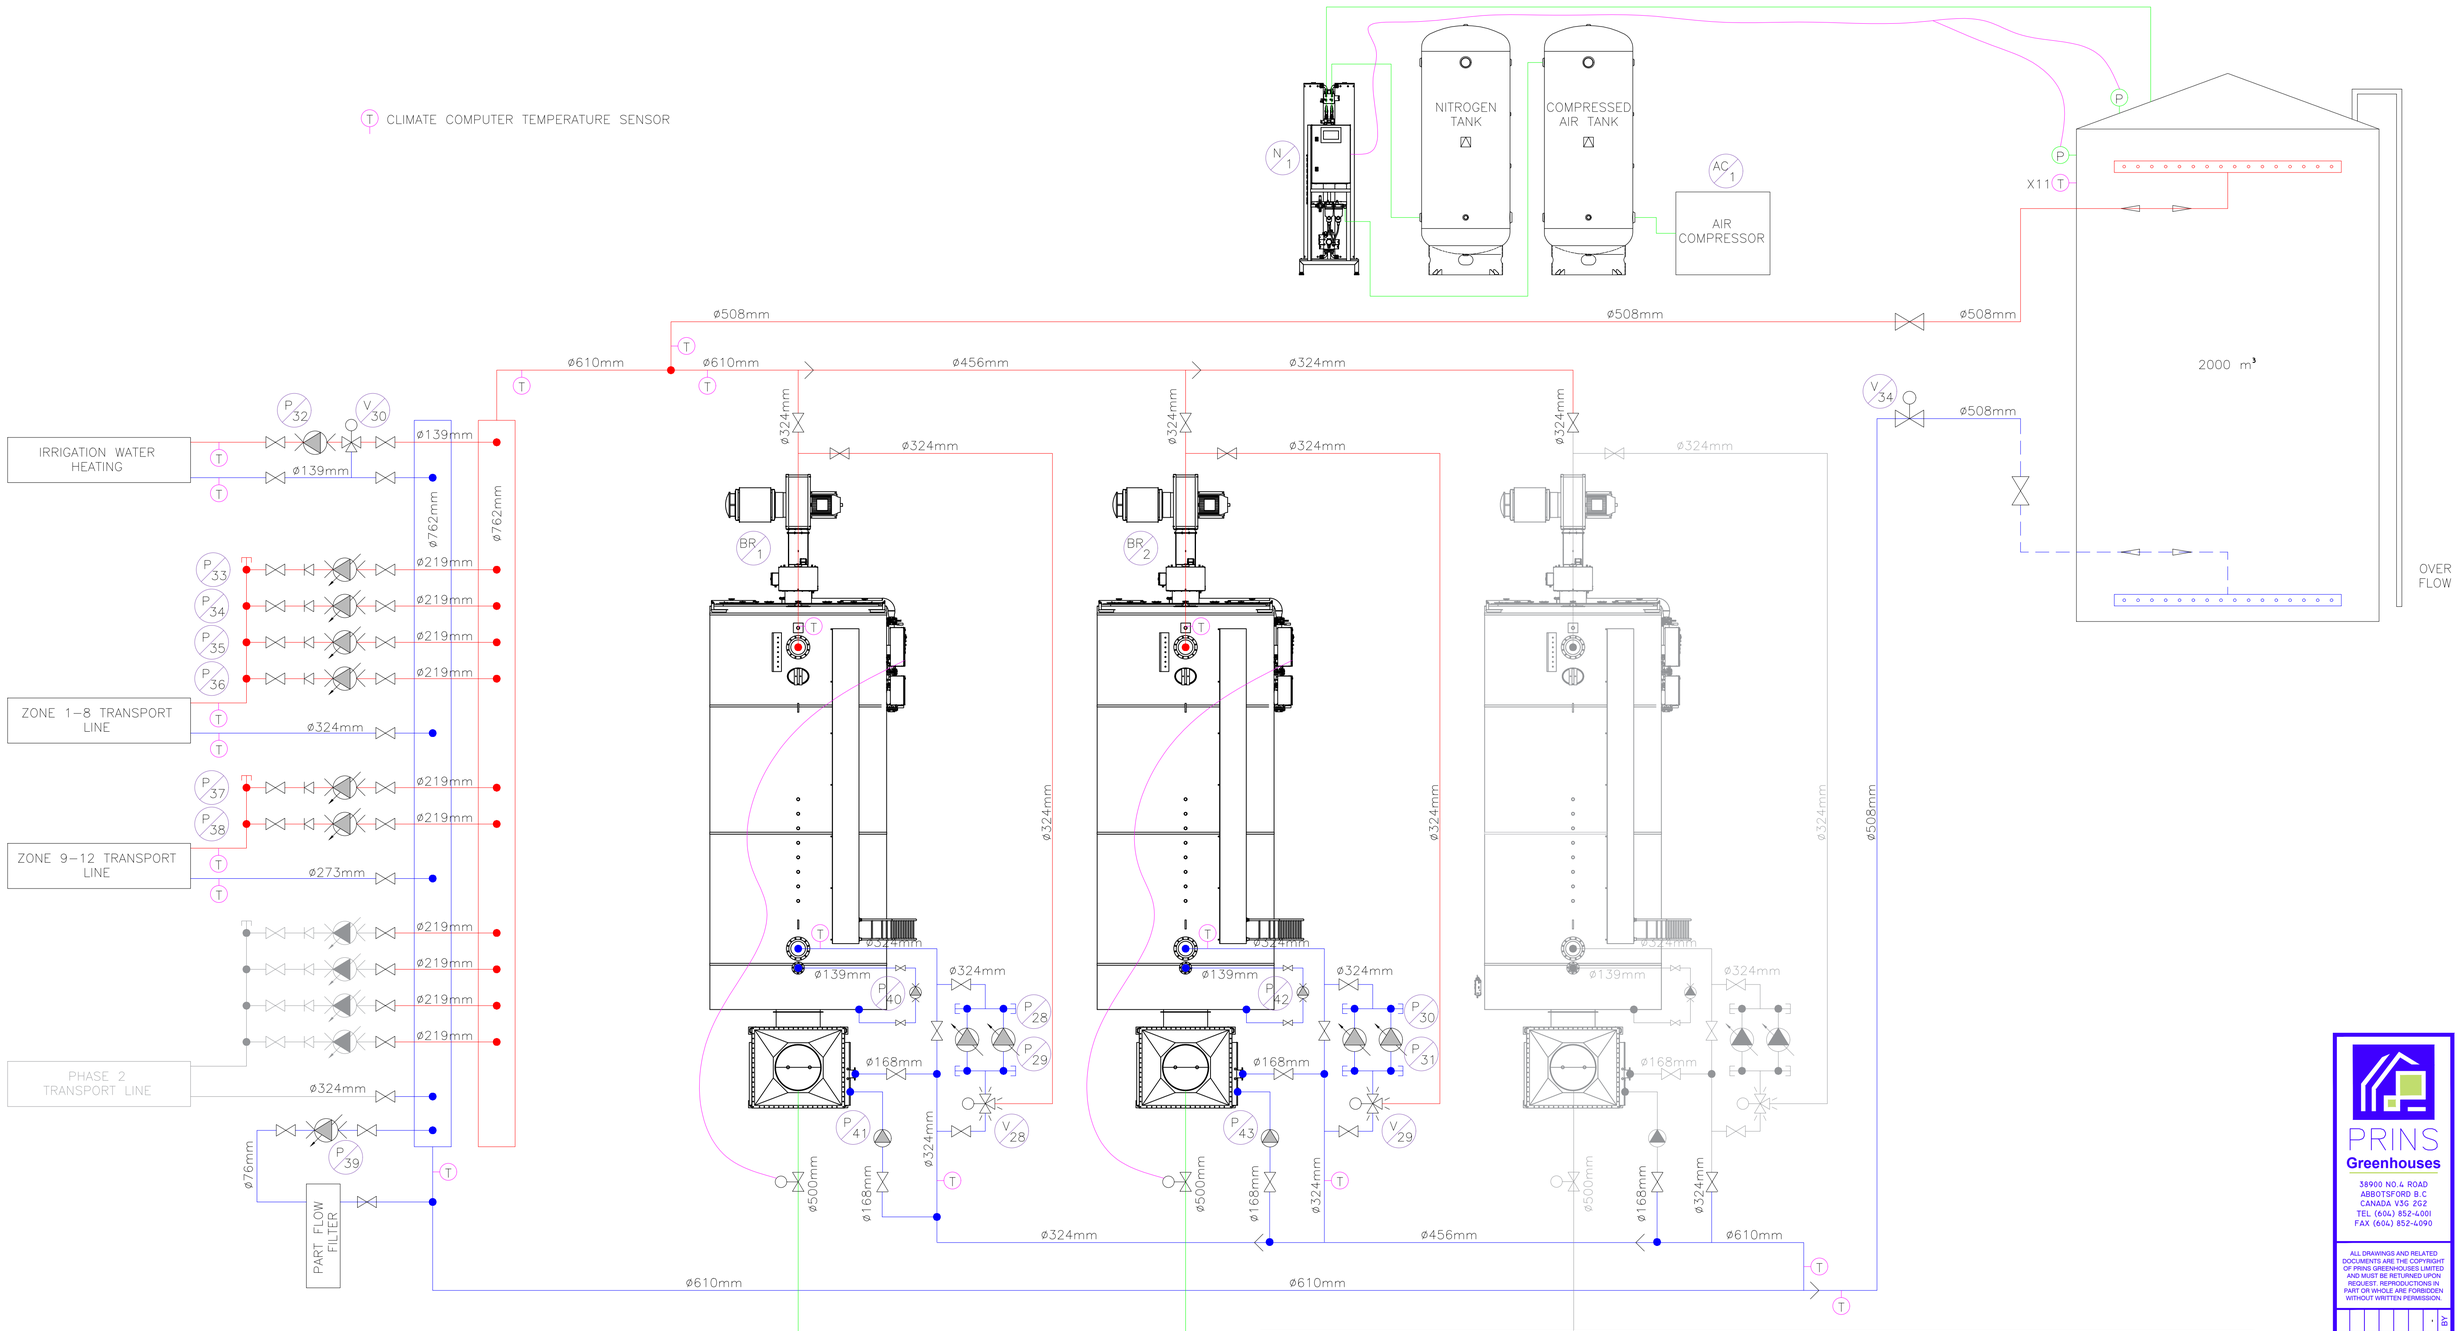

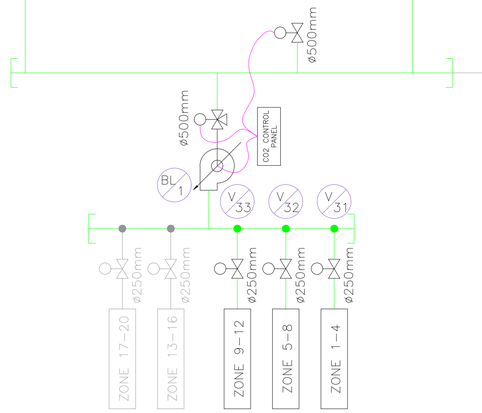

BOILER ROOM HEATING EQUIPMENT SCEHDULE

ID	SERVICE	MANUFACTURER	MODEL No.	MOTOR VOLTAGE	MOTOR kW	CONTROL	REMARKS
P28	BOILER 1 OPEN BUFFER PUMP 1	SPX	CLB200-160	575/3/60	4.00	VARIABLE SPEED	VFD BY OTHERS
P29	BOILER 1 OPEN BUFFER PUMP 2	SPX	CLB200-160	575/3/60	4.00	VARIABLE SPEED	VFD BY OTHERS
V28	BOILER 1 OPEN BUFFER MIXING VALVE	CENTRA	VMM40-24	24VAC		24 VAC FLOATING CONTROL	
P30	BOILER 2 OPEN BUFFER PUMP 1	SPX	CLB200-160	575/3/60	4.00	VARIABLE SPEED	VFD BY OTHERS
P31	BOILER 2 OPEN BUFFER PUMP 2	SPX	CLB200-160	575/3/60	4.00	VARIABLE SPEED	VFD BY OTHERS
V29	BOILER 2 OPEN BUFFER MIXING VALVE	CENTRA	VMM40-24	24VAC		24 VAC FLOATING CONTROL	
P32	IRRIGATION WATER HEATING PUMP	SPX	CL100-150-1.5/60	575/3/60	1.50	ON/OFF	
V30	IRRIGATION WATER HEATING MIXING VALVE	HONEYWELL	ML6421B3004	24VAC		24 VAC FLOATING CONTROL	
P33	NORTH TRANSPORT LINE PUMP 1	SPX	CL125-160	575/3/60	5.50	VARIABLE SPEED	VFD BY OTHERS
P34	NORTH TRANSPORT LINE PUMP 2	SPX	CL125-160	575/3/60	5.50	VARIABLE SPEED	VFD BY OTHERS
P35	NORTH TRANSPORT LINE PUMP 3	SPX	CL125-160	575/3/60	5.50	VARIABLE SPEED	VFD BY OTHERS
P36	NORTH TRANSPORT LINE PUMP 4	SPX	CL125-160	575/3/60	5.50	VARIABLE SPEED	VFD BY OTHERS
P37	SOUTH TRANSPORT LINE PUMP 1	SPX	CL125-160	575/3/60	5.50	VARIABLE SPEED	VFD BY OTHERS
P38	SOUTH TRANSPORT LINE PUMP 2	SPX	CL125-160	575/3/60	5.50	VARIABLE SPEED	VFD BY OTHERS
P39	PART FLOW FILTER PUMP	SPX	CL65-125-0.37/60	575/3/60	0.37	ON/OFF	
P40	BOILER 1 SHUNT PUMP	SPX	CL100-150-1.1/60	575/3/60	1.10	ON/OFF	
P41	BOILER 1 CONDENSER PUMP	SPX	CL150-125	575/3/60	2.20	ON/OFF	
P42	BOILER 2 SHUNT PUMP	SPX	CL100-150-1.1/60	575/3/60	1.10	ON/OFF	
P43	BOILER 2 CONDENSER PUMP	SPX	CL150-125	575/3/60	2.20	ON/OFF	
BR1	BOILER 1 BURNER FAN	ZANTINGH	RKB 12.0 ND MM G/O	575/3/60	45.00	FIDUFACE INTERFACE	
BR2	BOILER 2 BURNER FAN	ZANTINGH	RKB 12.0 ND MM G/O	575/3/60	45.00	FIDUFACE INTERFACE	
BL1	CO2 BLOWER UNIT	VAN DIJK	DSL500-150-60	575/3/60	15.00		
V31	CO2 ZONE VALVE Z1-4	BELIMO	SM24A	24VAC		24 VAC FLOATING CONTROL	
V32	CO2 ZONE VALVE Z5-8	BELIMO	SM24A	24VAC		24 VAC FLOATING CONTROL	
V33	CO2 ZONE VALVE Z9-12	BELIMO	SM24A	24VAC		24 VAC FLOATING CONTROL	
V34	HST RETURN SHUT-OFF VALVE	HABONIM	HABONIM C45DA WITH ASCO SOLENOID VALVE	24VAC		OPEN/CLOSE	
N1	PRESSCON NITROGEN GENERATOR	PRESSCON	VERNIT 12.0 N2 PREMIUM	110/1/60			
AC1	AIR COMPRESSOR	TBD	TBD	575/3/60	TBD		BY SCHENCK

PRINS Greenhouses
38900 NO.4 ROAD
ABBOTSFORD B.C
CANADA V3G 2G2
TEL (604) 852-4001
FAX (604) 852-4090

ALL DRAWINGS AND RELATED DOCUMENTS ARE THE COPYRIGHT OF PRINS GREENHOUSES LIMITED AND MUST BE RETURNED UPON REQUEST. REPRODUCTIONS IN PART OR WHOLE ARE FORBIDDEN WITHOUT WRITTEN PERMISSION.

REV	ACTION	DATE	BY
-	-	-	-

CUSTOMER: SCHENCK FARMS

TITLE: HEATING SCHEMATIC

DATE: JAN 28, 2025
DRAWN: MR
CHECKED: MR
PROJECT: 24-4591
SHEET No.: HE-300
REV.: -