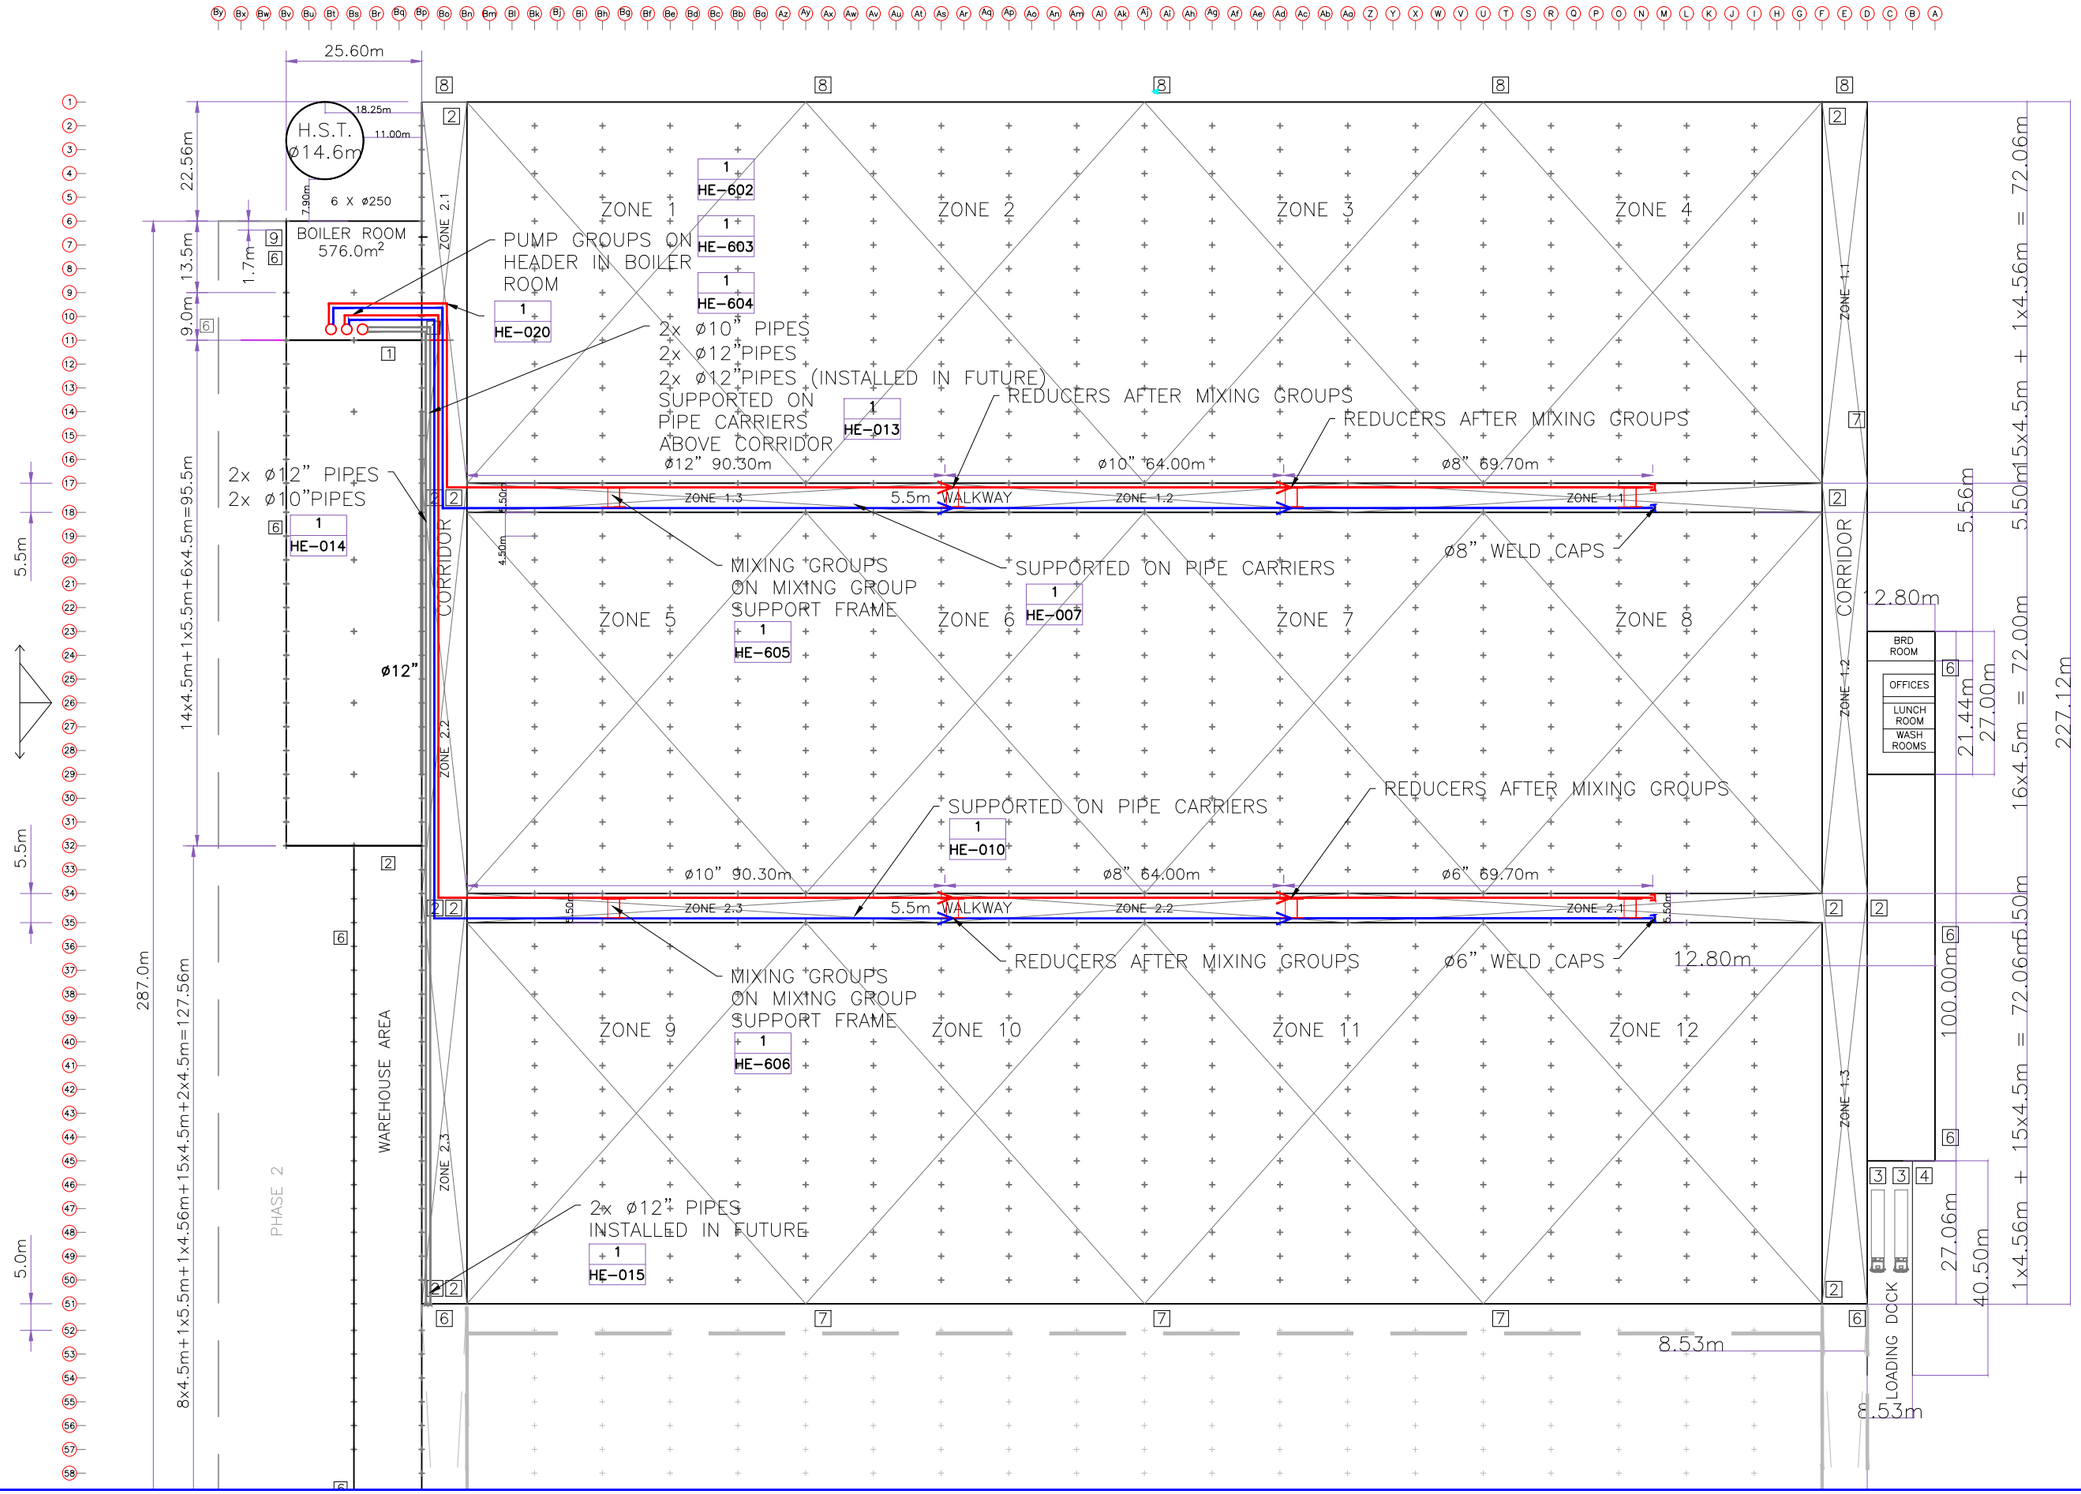

PRINS GREENHOUSES

38900 NO.4 ROAD
ABBOTSFORD, B.C.
CANADA V3G 2G2
TEL (604) 852-4001
FAX (604) 852-4090

3500 SOUTH SERVICE ROAD
VINELAND STATION, ON.
CANADA L0R 2E0
TEL (905) 562-4411
FAX (905) 562-5533

ALL DRAWINGS AND RELATED DOCUMENTS ARE THE COPYRIGHT OF PRINS GREENHOUSES LIMITED AND MUST BE RETURNED UPON REQUEST. REPRODUCTIONS IN PART OR WHOLE ARE FORBIDDEN WITHOUT WRITTEN PERMISSION.

REV	ACTION	DATE	BY
A	CALL OUTS REVISED	06/13/25	DM

CUSTOMER: SCHENCK FARMS

TITLE: MAIN TRANSPORT LINE LAUYOUT

DATE: JUN 10/25

DRAWN: DM | CHECKED: MR

PROJECT: 24-4591

SHEET No. HE-601 | REV. A

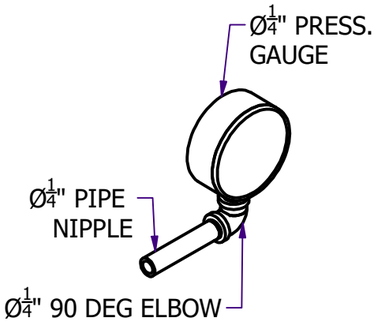

PRESS. GAUGE ASSEMBLY

SCALE: 1/4

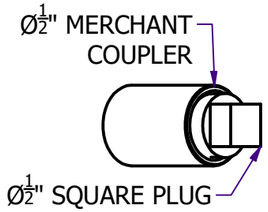

TEMP. SENSOR ASSEMBLY
SCALE: 1/2

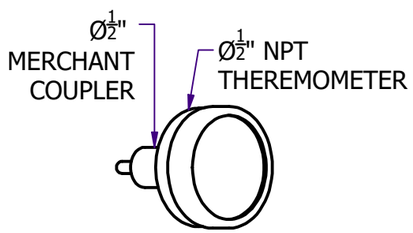

THERMOMETER ASSEMBLY
SCALE: 1/4

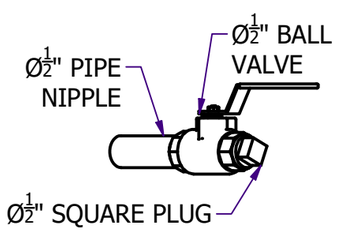

DRAIN VALVE ASSEMBLY

SCALE: 1/4

CL 125-160,5.5 Kw, ND10< 1750, 575/3/60	
QTY	COMPONENT
2	WELD NECK FLANGE ND16 NW125/139.7
2	GASKET KORO HD ND16 125
8	HEXAGONAL BOLT 8.8 M16 x 140 GALV.
8	HEXAGONAL NUT 8 VERZINKT M16

NON-RETURN VALVE DC DN 200	
QTY	COMPONENT
2	WELD NECK FLANGE ND 16 NW 200/219.1
2	GASKET KORO HD ND 16 200
12	HEXAGONAL BOLT 8.8 M20 x 160 GALV.
12	HEXAGONAL NUT 8 VERZINKT M 16

BUTTERFLY VALVE Z011-A1 DN 200	
QTY	COMPONENT
2	WELD NECK FLANGE ND6 NW 200/219.1
8	HEXAGONAL BOLT 8.8 M16 x 120 GALV.
8	HEXAGONAL NUT 8 VERZINKT M16

BUTTERFLY VALVE Z011-A1 DN300	
QTY	COMPONENT
2	WELD NECK FLANGE ND6 NW300/323.9
12	HEXAGONAL BOLT 8.8 M16 x 140 GALV.
12	HEXAGONAL NUT 8 VERZINKT M16

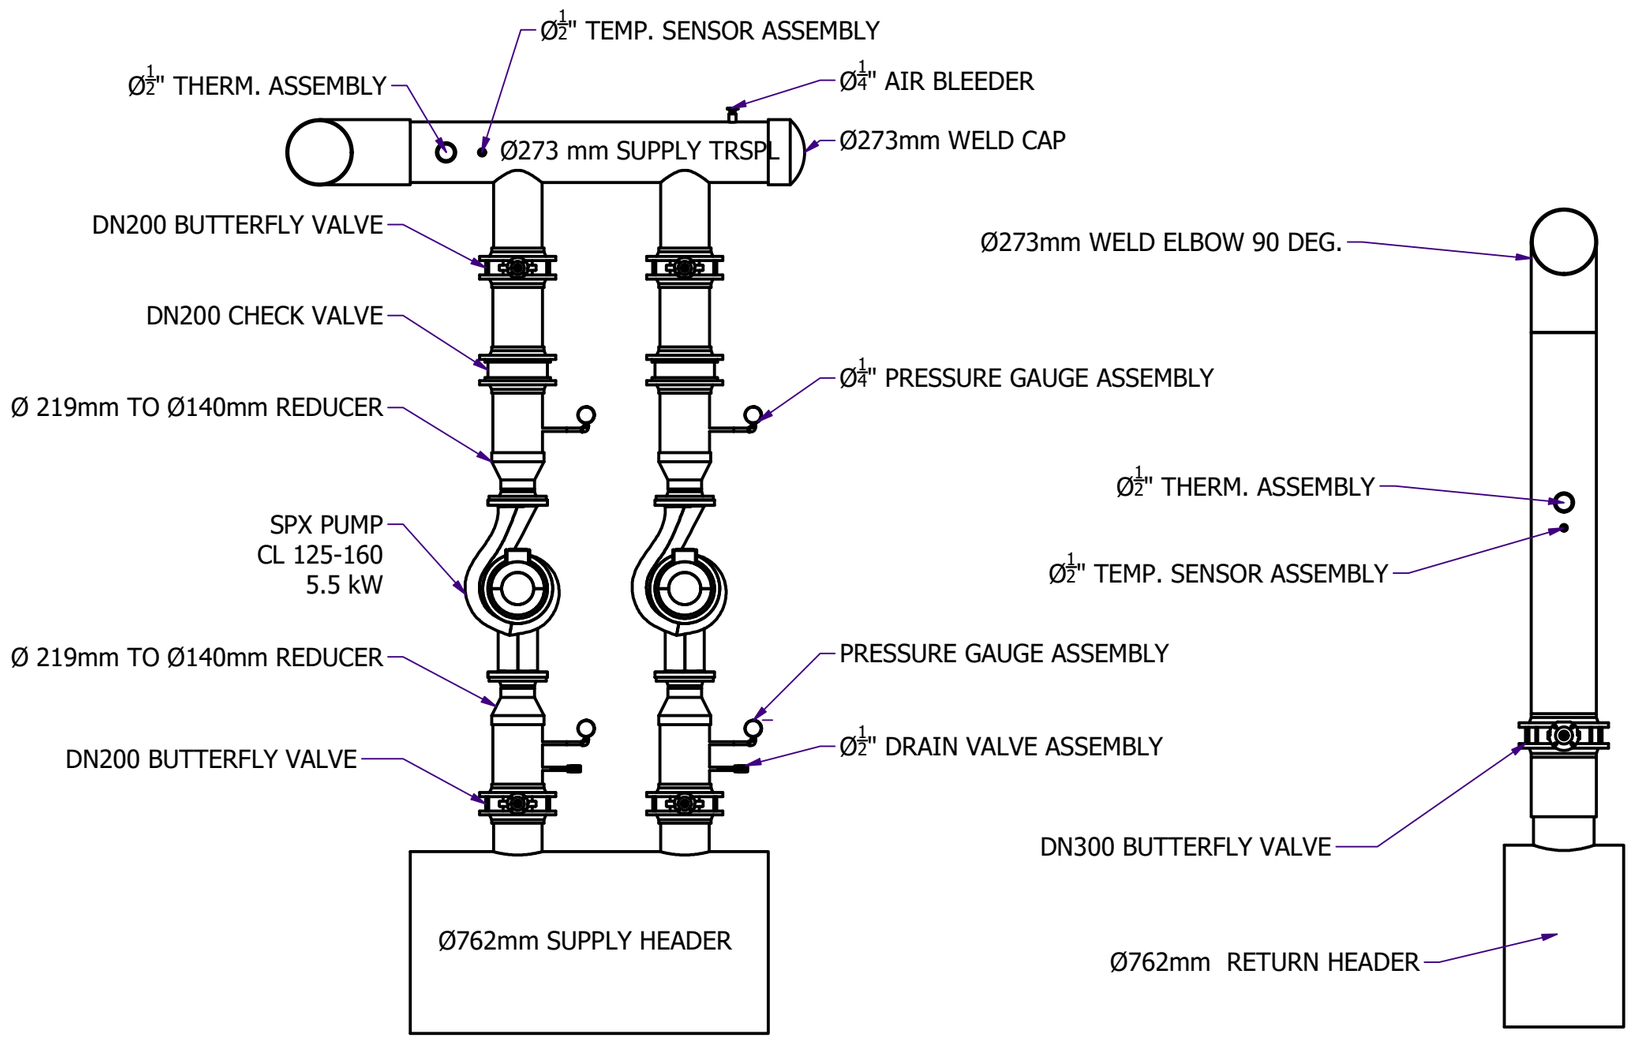

PRINS GREENHOUSES

38900 NO.4 ROAD
ABBOTSFORD, B.C.
CANADA V3G 2G2
TEL (604) 852-4001
FAX (604) 852-4090

3500 SOUTH SERVICE ROAD
VINELAND STATION, ON.
CANADA L0R 2E0
TEL (905) 562-4411
FAX (905) 562-5533

ALL DRAWINGS AND RELATED DOCUMENTS ARE THE COPYRIGHT OF PRINS GREENHOUSES LIMITED AND MUST BE RETURNED UPON REQUEST. REPRODUCTIONS IN PART OR WHOLE ARE FORBIDDEN WITHOUT WRITTEN PERMISSION.

REV	ACTION	DATE	BY
A	RETURN CONN. ADDED	06/12/025	DM

CUSTOMER: SCHENCK FARMS

TITLE: ZONE 9-12 TRSPL PUMP GROUP

DATE: 06/10/25

DRAWN: DM CHECKED: MR

PROJECT: 24-4591

SHEET No. HE-602

REV. A

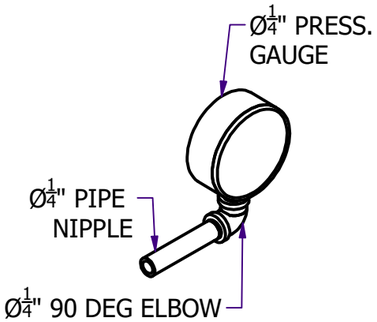

PRESS. GAUGE ASSEMBLY
SCALE: 1/4

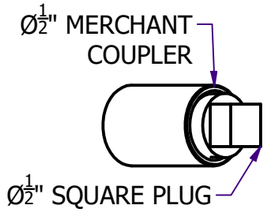

TEMP. SENSOR ASSEMBLY
SCALE: 1/2

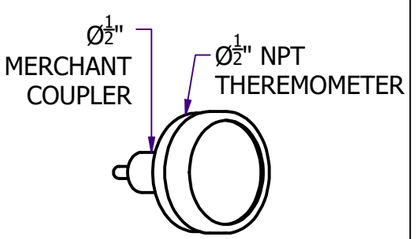

THERMOMETER ASSEMBLY
SCALE: 1/4

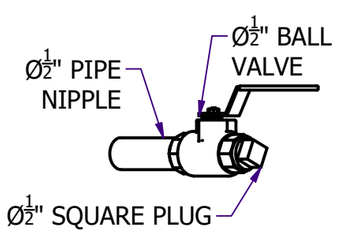

DRAIN VALVE ASSEMBLY
SCALE: 1/4

CL 125-160,5.5 Kw, ND10< 1750, 575/3/60	
QTY	COMPONENT
2	WELD NECK FLANGE ND16 NW125/139.7
2	GASKET KORO HD ND16 125
8	HEXAGONAL BOLT 8.8 M16 x 140 GALV.
8	HEXAGONAL NUT 8 VERZINKT M16

NON-RETURN VALVE DC DN 200	
QTY	COMPONENT
2	WELD NECK FLANGE ND 16 NW 200/219.1
2	GASKET KORO HD ND 16 200
12	HEXAGONAL BOLT 8.8 M20 x 160 GALV.
12	HEXAGONAL NUT 8 VERZINKT M 16

BUTTERFLY VALVE Z011-A1 DN 200	
QTY	COMPONENT
2	WELD NECK FLANGE ND6 NW 200/219.1
8	HEXAGONAL BOLT 8.8 M16 x 120 GALV.
8	HEXAGONAL NUT 8 VERZINKT M16

BUTTERFLY VALVE Z011-A1 DN300	
QTY	COMPONENT
2	WELD NECK FLANGE ND6 NW300/323.9
12	HEXAGONAL BOLT 8.8 M16 x 140 GALV.
12	HEXAGONAL NUT 8 VERZINKT M16

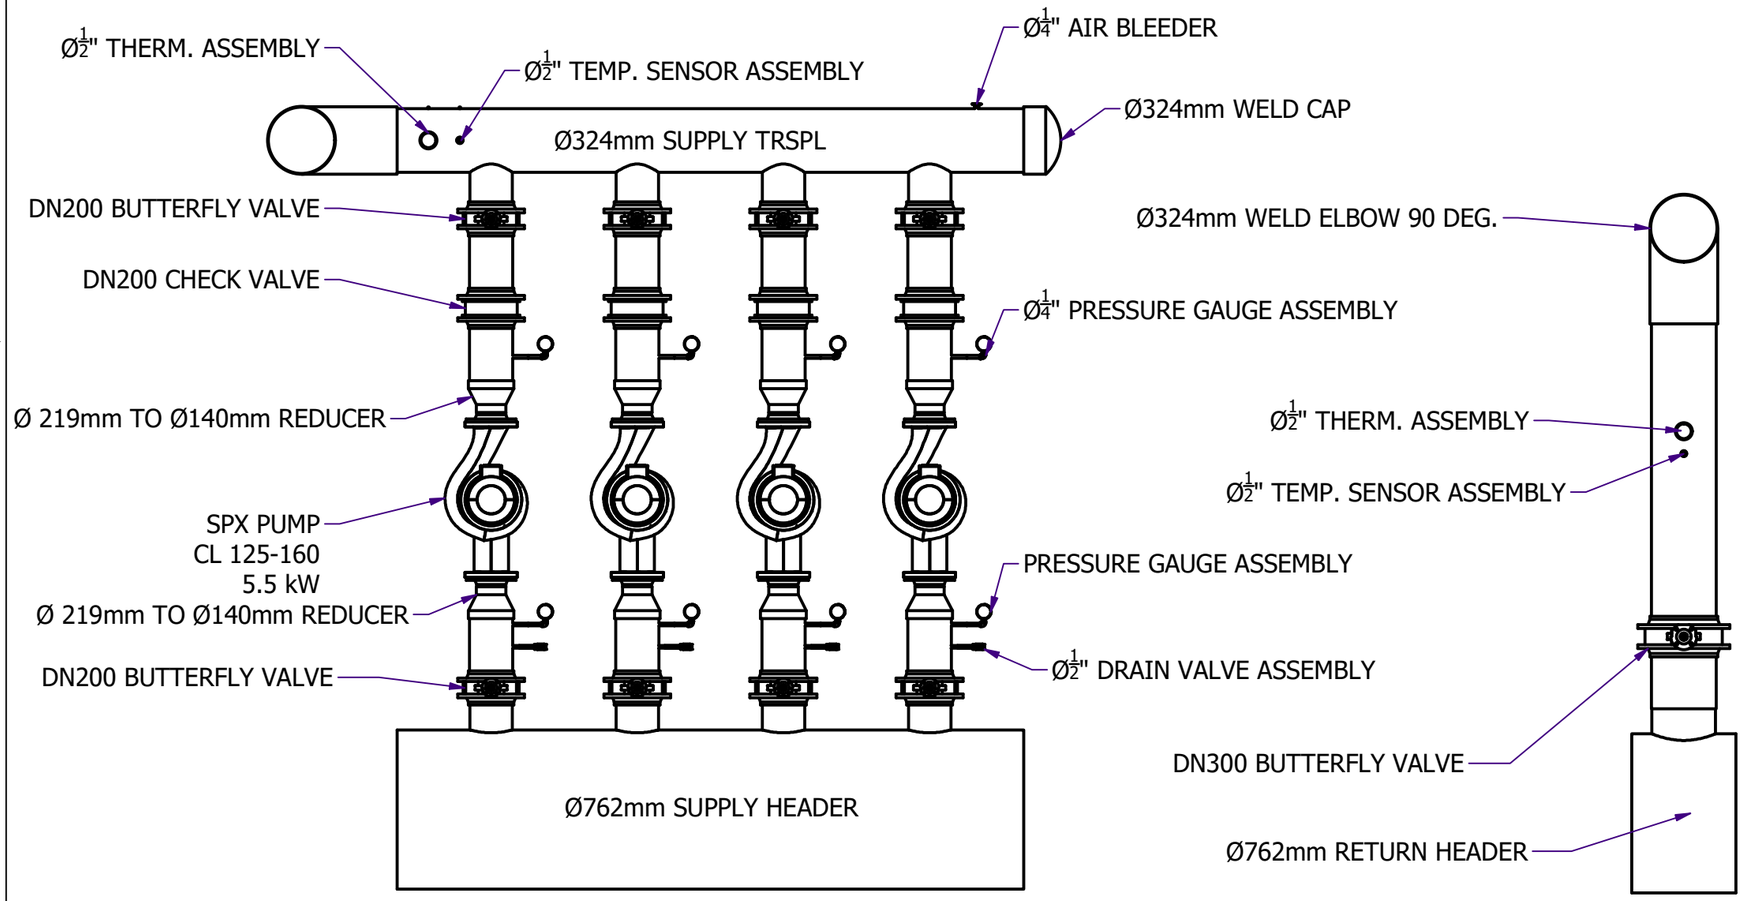

PRINS GREENHOUSES

38900 NO.4 ROAD
ABBOTSFORD, B.C.
CANADA V3G 2G2
TEL (604) 852-4001
FAX (604) 852-4090

3500 SOUTH SERVICE ROAD
VINELAND STATION, ON.
CANADA L0R 2E0
TEL (905) 562-4411
FAX (905) 562-5533

ALL DRAWINGS AND RELATED DOCUMENTS ARE THE COPYRIGHT OF PRINS GREENHOUSES LIMITED AND MUST BE RETURNED UPON REQUEST. REPRODUCTIONS IN PART OR WHOLE ARE FORBIDDEN WITHOUT WRITTEN PERMISSION.

REV	ACTION	DATE	BY
A	RETURN CONN. ADDED	06/12/25	DM

CUSTOMER: SCHENCK FARMS

TITLE: ZONE 1-8 TRSPL PUMP GROUP

DATE: 06/10/25

DRAWN: DM CHECKED: MR

PROJECT: 24-4591

SHEET No. HE-603 REV. A

BUTTERFLY VALVE Z011-A1 DN 200	
QTY	COMPONENT
2	WELD NECK FLANGE ND6 NW 200/219.1
8	HEXAGONAL BOLT 8.8 M16 x 120 GALV.
8	HEXAGONAL NUT 8 VERZINKT M16

BUTTERFLY VALVE Z011-A1 DN 300	
QTY	COMPONENT
2	WELD NECK FLANGE ND6 NW 300/323.9
8	HEXAGONAL BOLT 8.8 M16 x 140 GALV.
8	HEXAGONAL NUT 8 VERZINKT M16

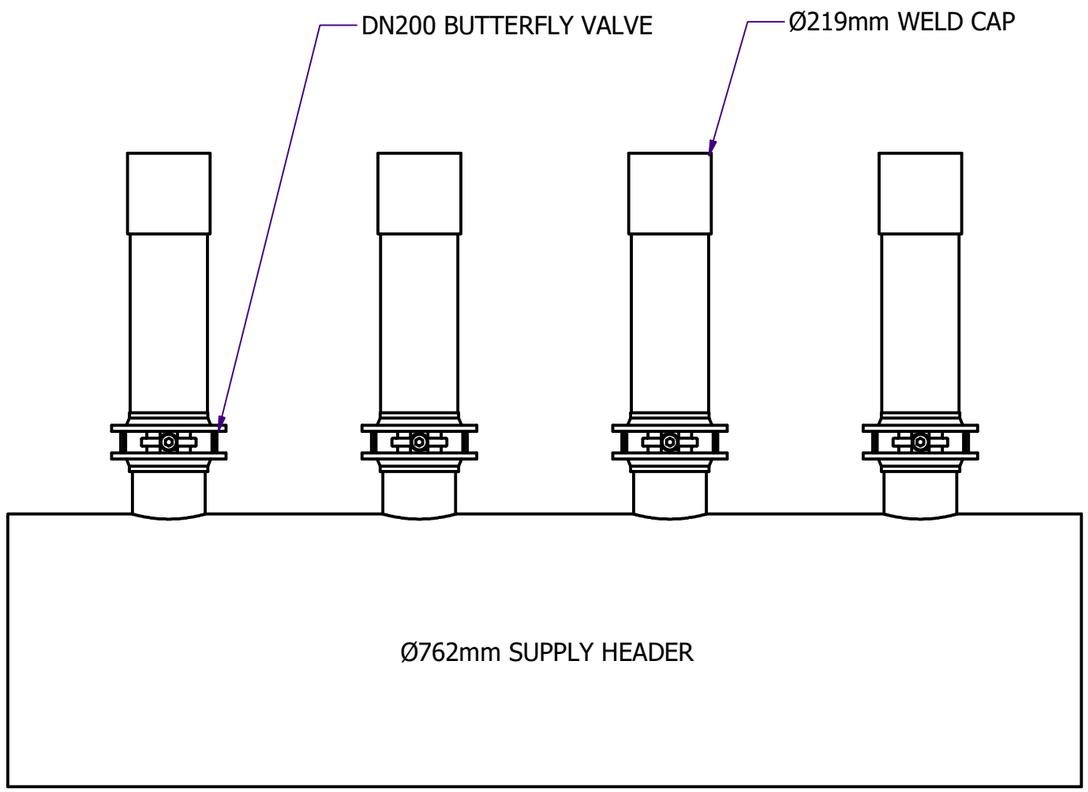

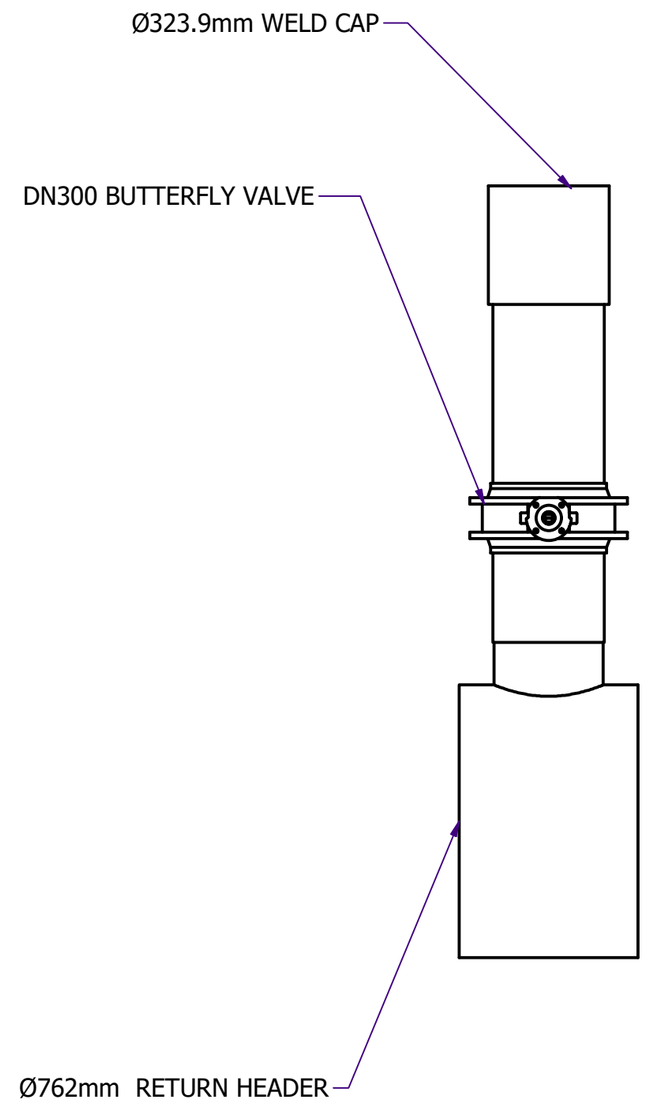

PRINS
GREENHOUSES

38900 NO.4 ROAD
ABBOTSFORD, B.C.
CANADA V3G 2G2
TEL (604) 852-4001
FAX (604) 852-4090

3500 SOUTH SERVICE ROAD
VINELAND STATION, ON.
CANADA L0R 2E0
TEL (905) 562-4411
FAX (905) 562-5533

ALL DRAWINGS AND RELATED DOCUMENTS ARE THE COPYRIGHT OF PRINS GREENHOUSES LIMITED AND MUST BE RETURNED UPON REQUEST. REPRODUCTIONS IN PART OR WHOLE ARE FORBIDDEN WITHOUT WRITTEN PERMISSION.

REV	ACTION	DATE	BY

CUSTOMER: SCHENCK FARMS

TITLE: FUTURE TRSPL PUMP STUBS

DATE: 06/11/25

DRAWN: DM | CHECKED:

PROJECT: 24-4591

SHEET No. HE-604 | REV.

NOTE: ZONES 1 & 5 SHOWN

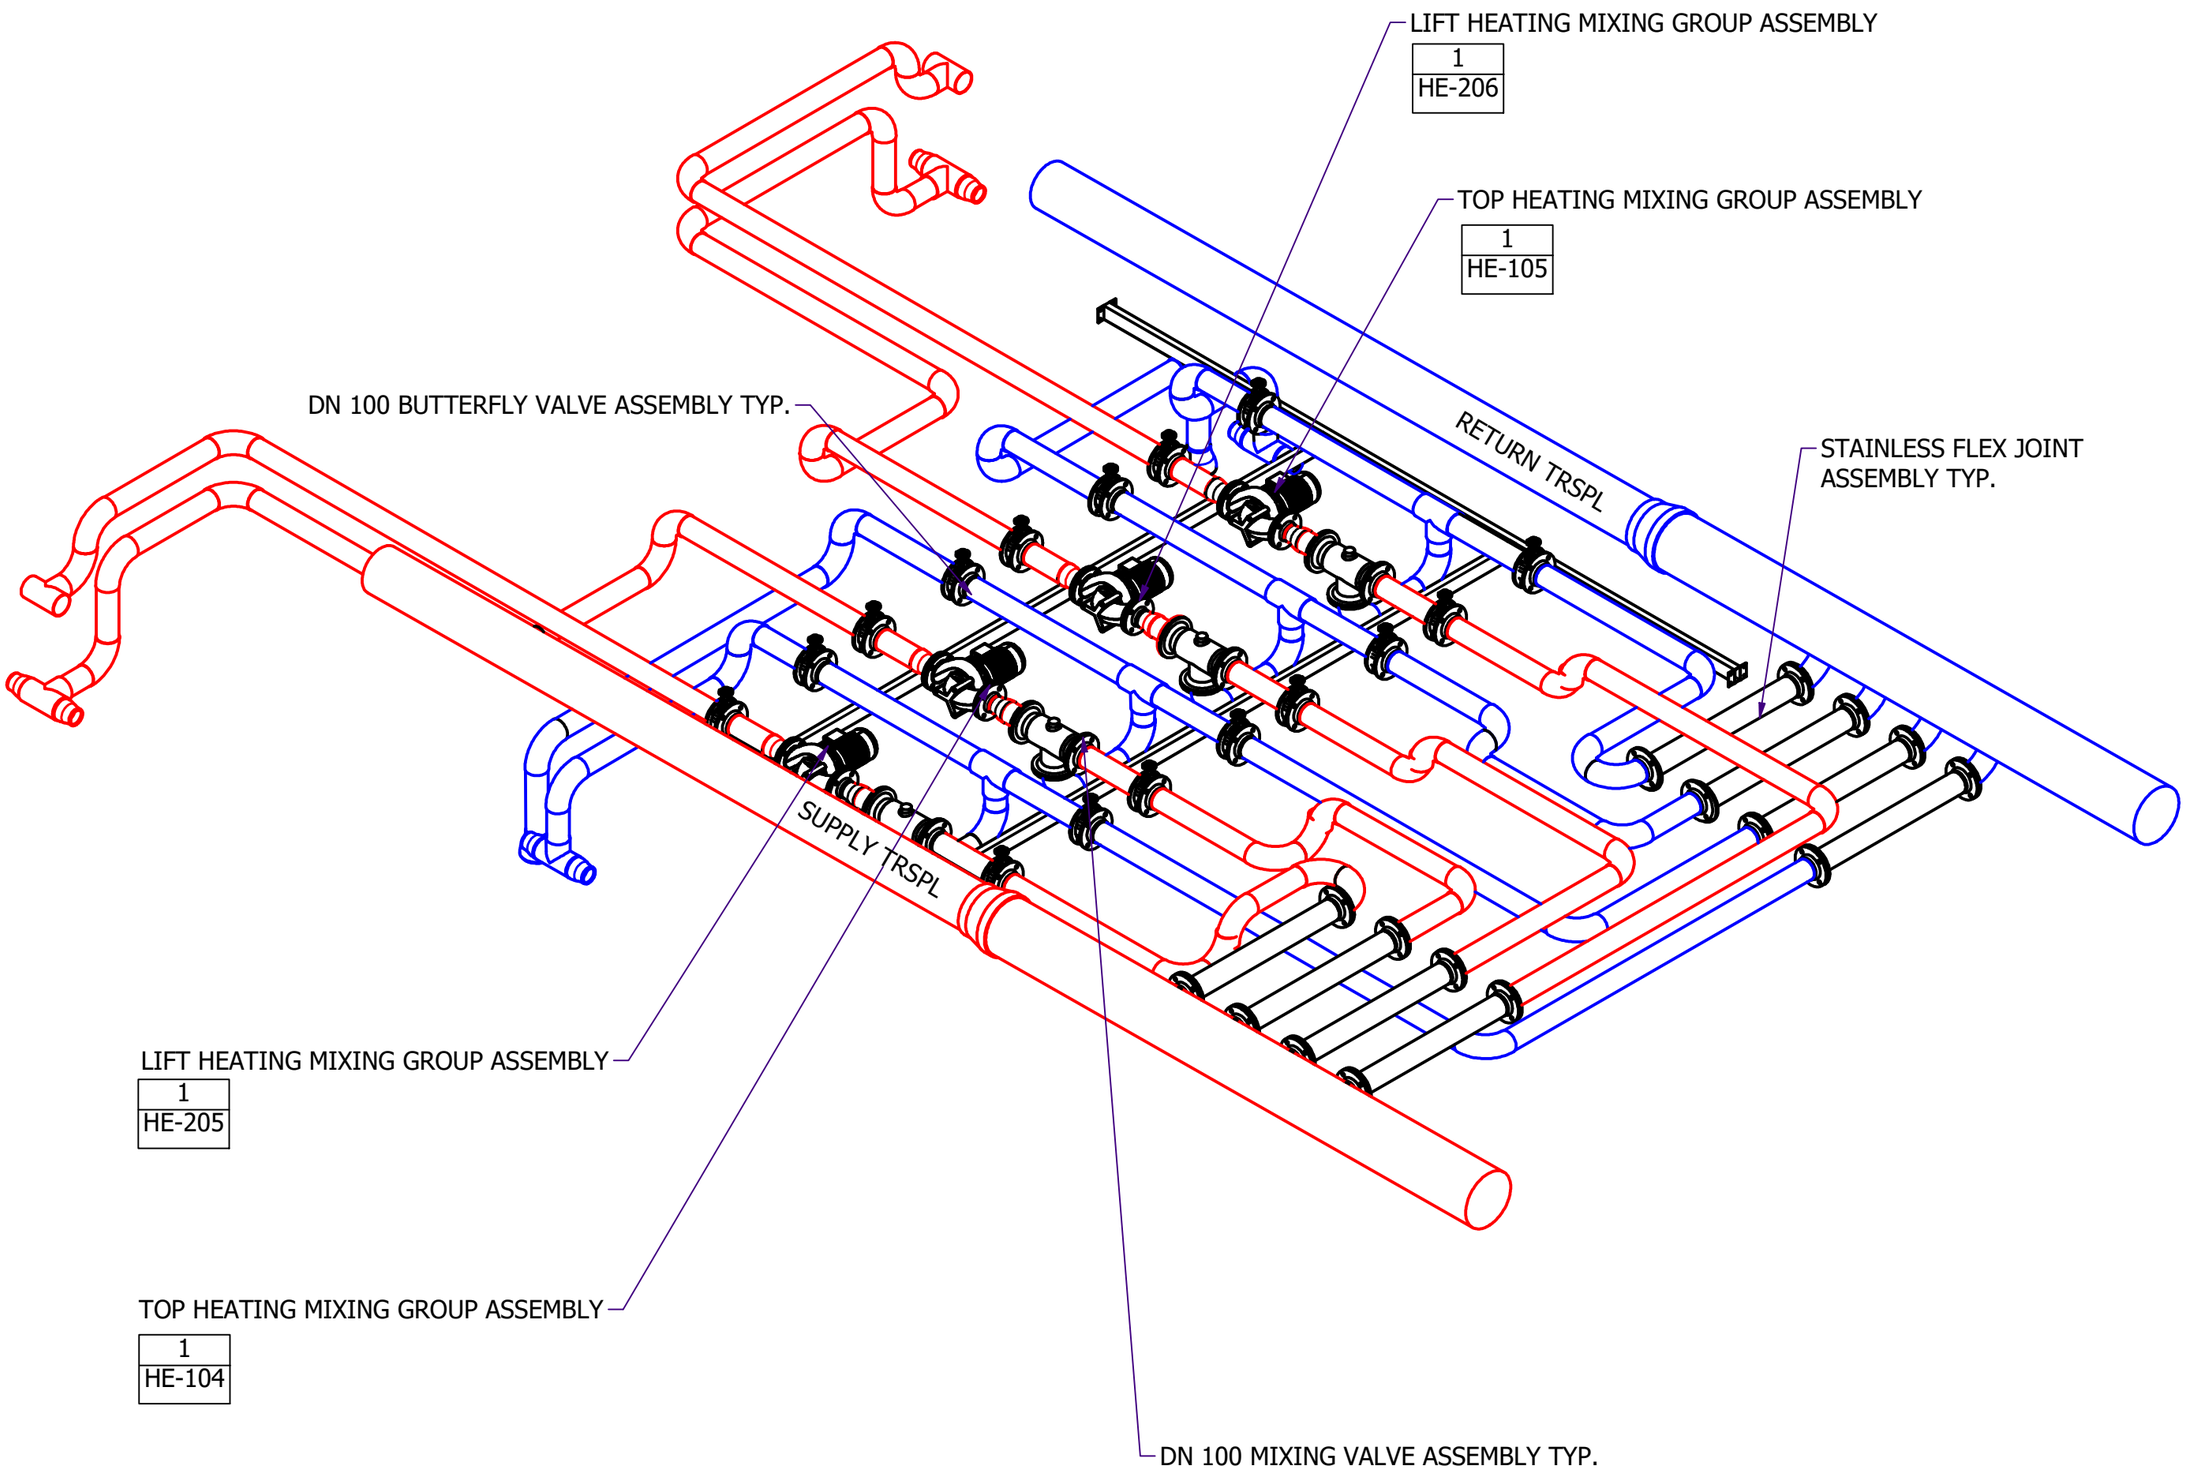

PRINS GREENHOUSES

38900 NO.4 ROAD
ABBOTSFORD, B.C.
CANADA V3G 2G2
TEL (604) 852-4001
FAX (604) 852-4090

3500 SOUTH SERVICE ROAD
VINELAND STATION, ON.
CANADA L0R 2E0
TEL (905) 562-4411
FAX (905) 562-5533

ALL DRAWINGS AND RELATED DOCUMENTS ARE THE COPYRIGHT OF PRINS GREENHOUSES LIMITED AND MUST BE RETURNED UPON REQUEST. REPRODUCTIONS IN PART OR WHOLE ARE FORBIDDEN WITHOUT WRITTEN PERMISSION.

REV	ACTION	DATE	BY
A	TRSPL RED. ADDED	06/11/25	DM

CUSTOMER: SCHENCK FARMS

TITLE: ZONE 1-8 MIXING GROUPS ON SUPPORT FRAME

DATE: 06/09/25

DRAWN: DM | CHECKED: MR

PROJECT: 24-4591

SHEET No. HE-605 | REV. A

NOTE: ZONE 9 SHOWN

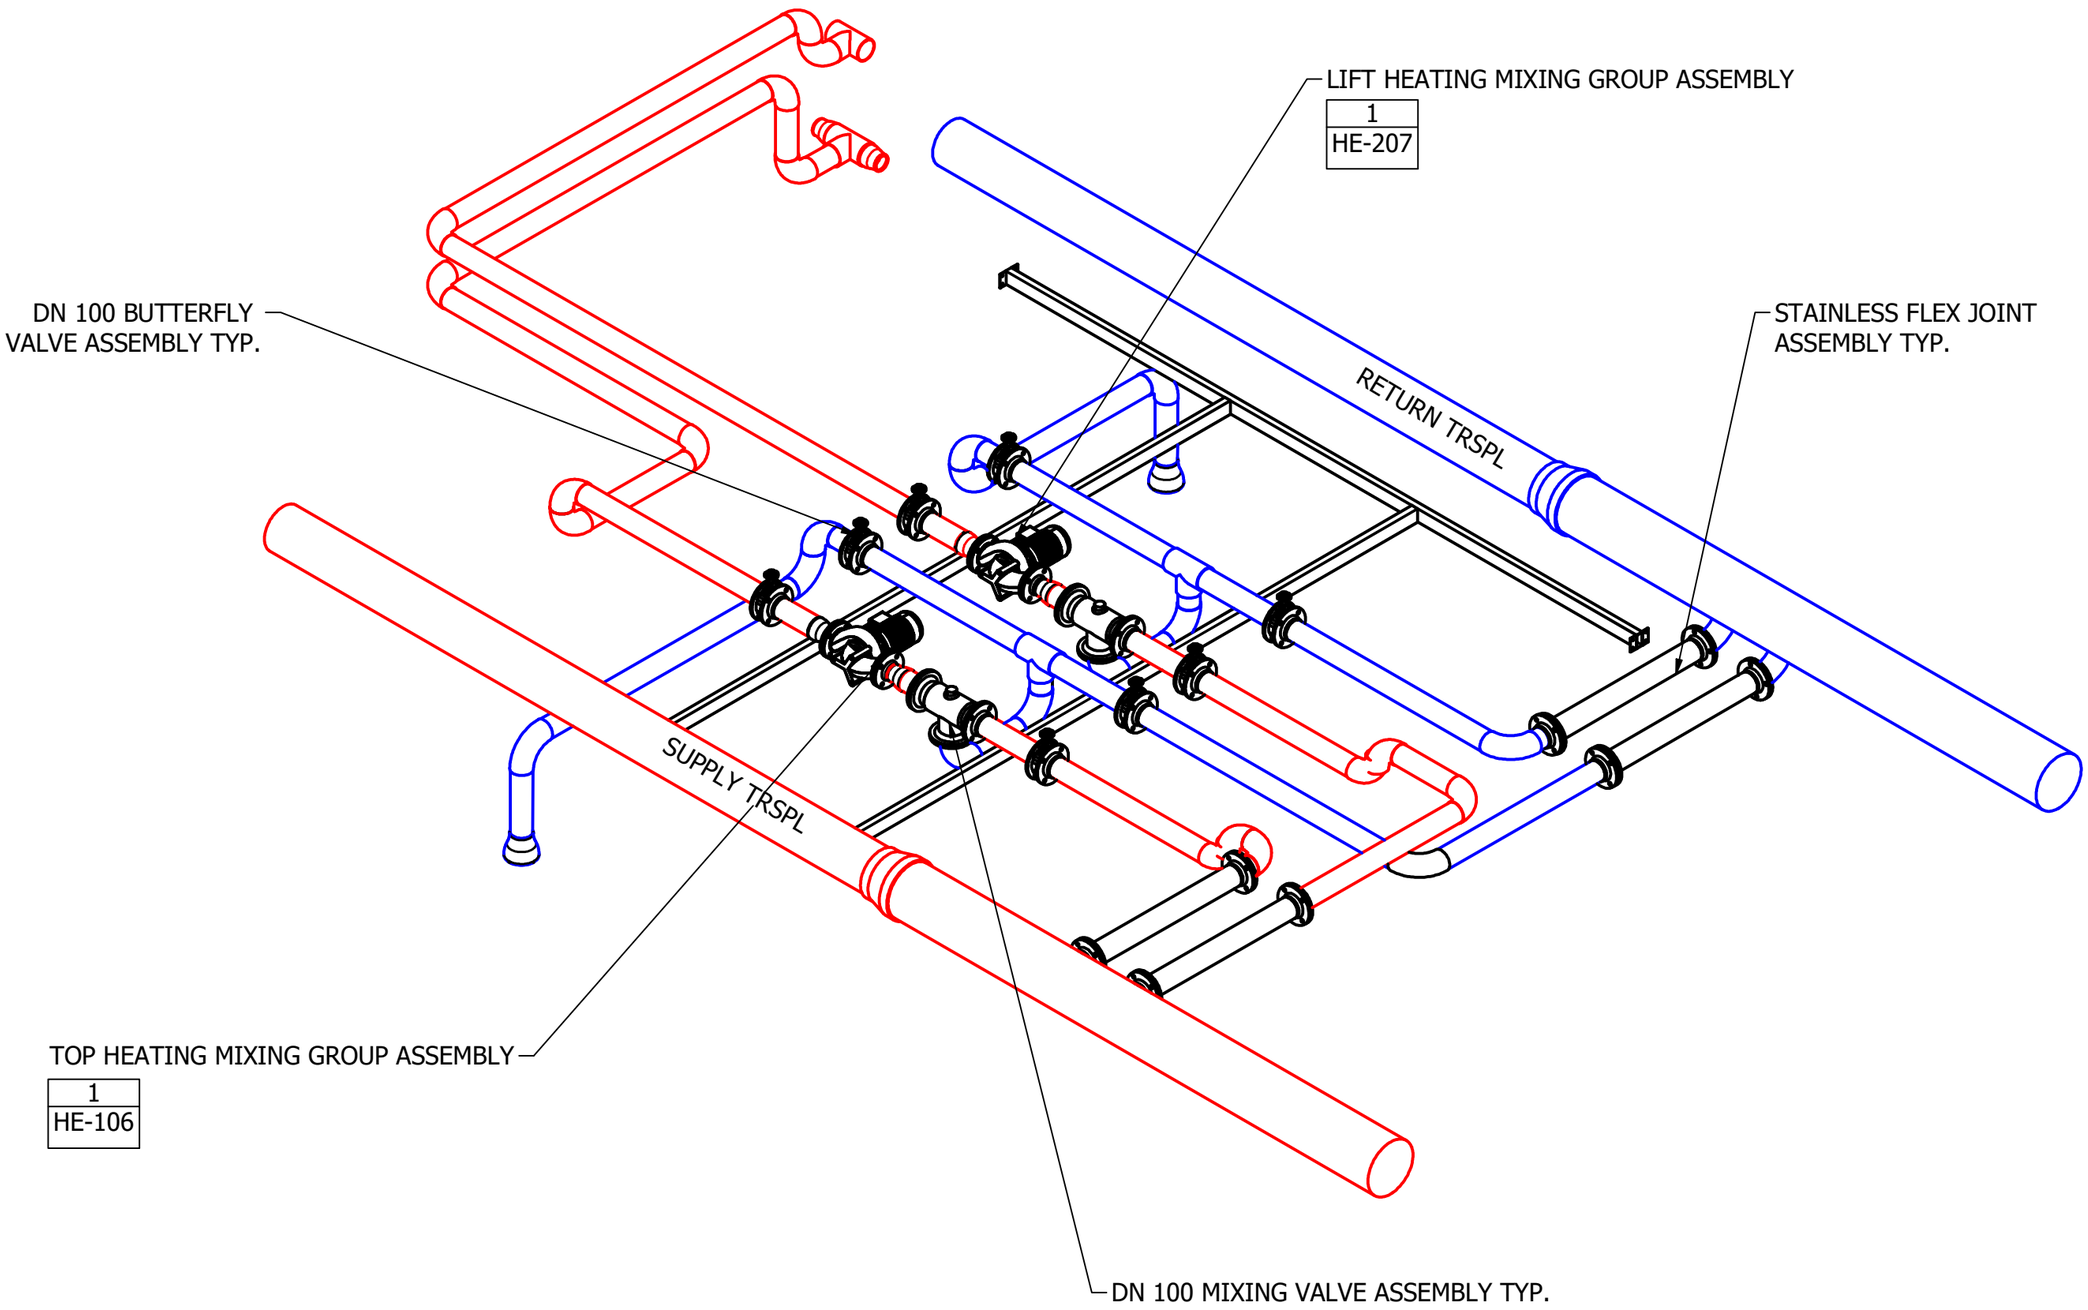

PRINS GREENHOUSES

38900 NO.4 ROAD
ABBOTSFORD, B.C.
CANADA V3G 2G2
TEL (604) 852-4001
FAX (604) 852-4090

3500 SOUTH SERVICE ROAD
VINELAND STATION, ON.
CANADA L0R 2E0
TEL (905) 562-4411
FAX (905) 562-5533

ALL DRAWINGS AND RELATED DOCUMENTS ARE THE COPYRIGHT OF PRINS GREENHOUSES LIMITED AND MUST BE RETURNED UPON REQUEST. REPRODUCTIONS IN PART OR WHOLE ARE FORBIDDEN WITHOUT WRITTEN PERMISSION.

REV	ACTION	DATE	BY
A	TRSPL RED ADDED	06/11/25	DM

CUSTOMER: SCHENCK FARMS

TITLE: ZONE 9-12 MIXING GROUPS ON SUPPORT FRAME

DATE: 06/09/25

DRAWN: DM | CHECKED: MR

PROJECT: 24-4591

SHEET No. HE-606 | REV. A

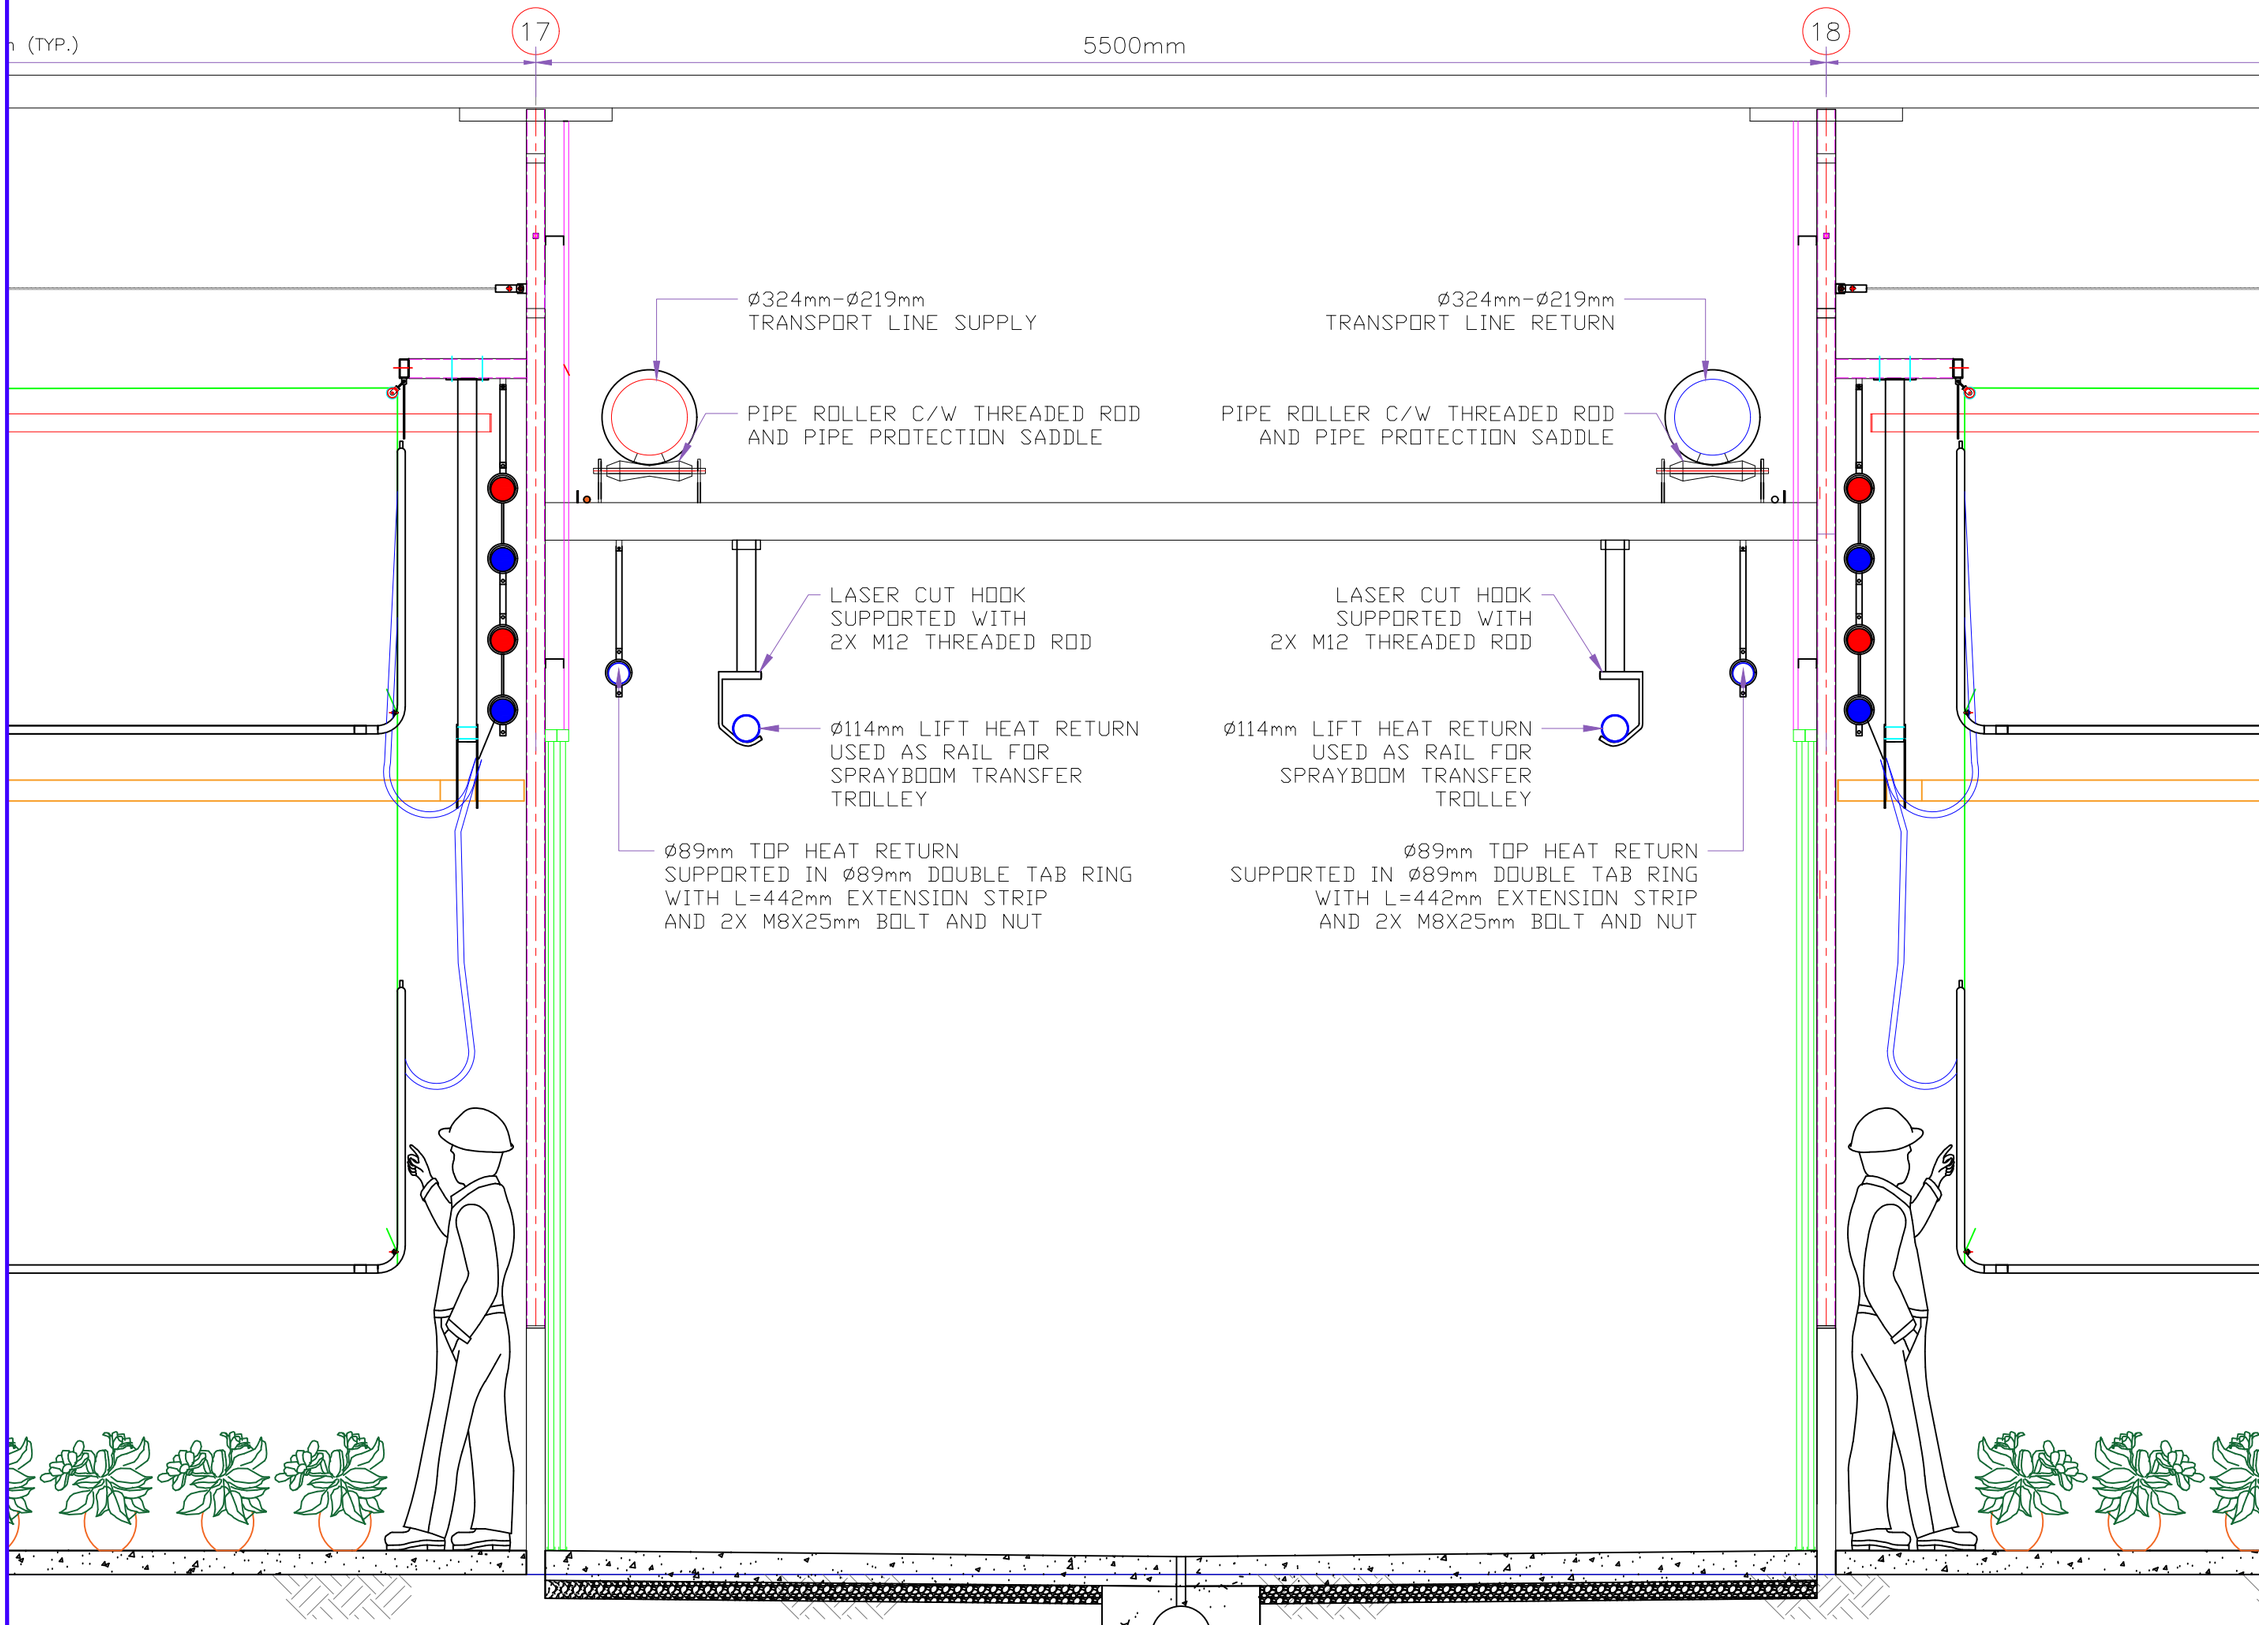

PRINS
Greenhouses
38900 NO.4 ROAD
ABBOTSFORD B.C
CANADA V3G 2G2
TEL (604) 852-4001
FAX (604) 852-4090

ALL DRAWINGS AND RELATED DOCUMENTS ARE THE COPYRIGHT OF PRINS GREENHOUSES LIMITED AND MUST BE RETURNED UPON REQUEST. REPRODUCTIONS IN PART OR WHOLE ARE FORBIDDEN WITHOUT WRITTEN PERMISSION.

REV	ACTION	DATE	BY

CUSTOMER
SCHENCK FARMS

TITLE
WALKWAY CROSS SECTION AT GL17/18

DATE: FEB 23, 2024
DRAWN: MR
CHECKED: MR
PROJECT: 24-4591

SHEET No.	REV.
HE-007	-

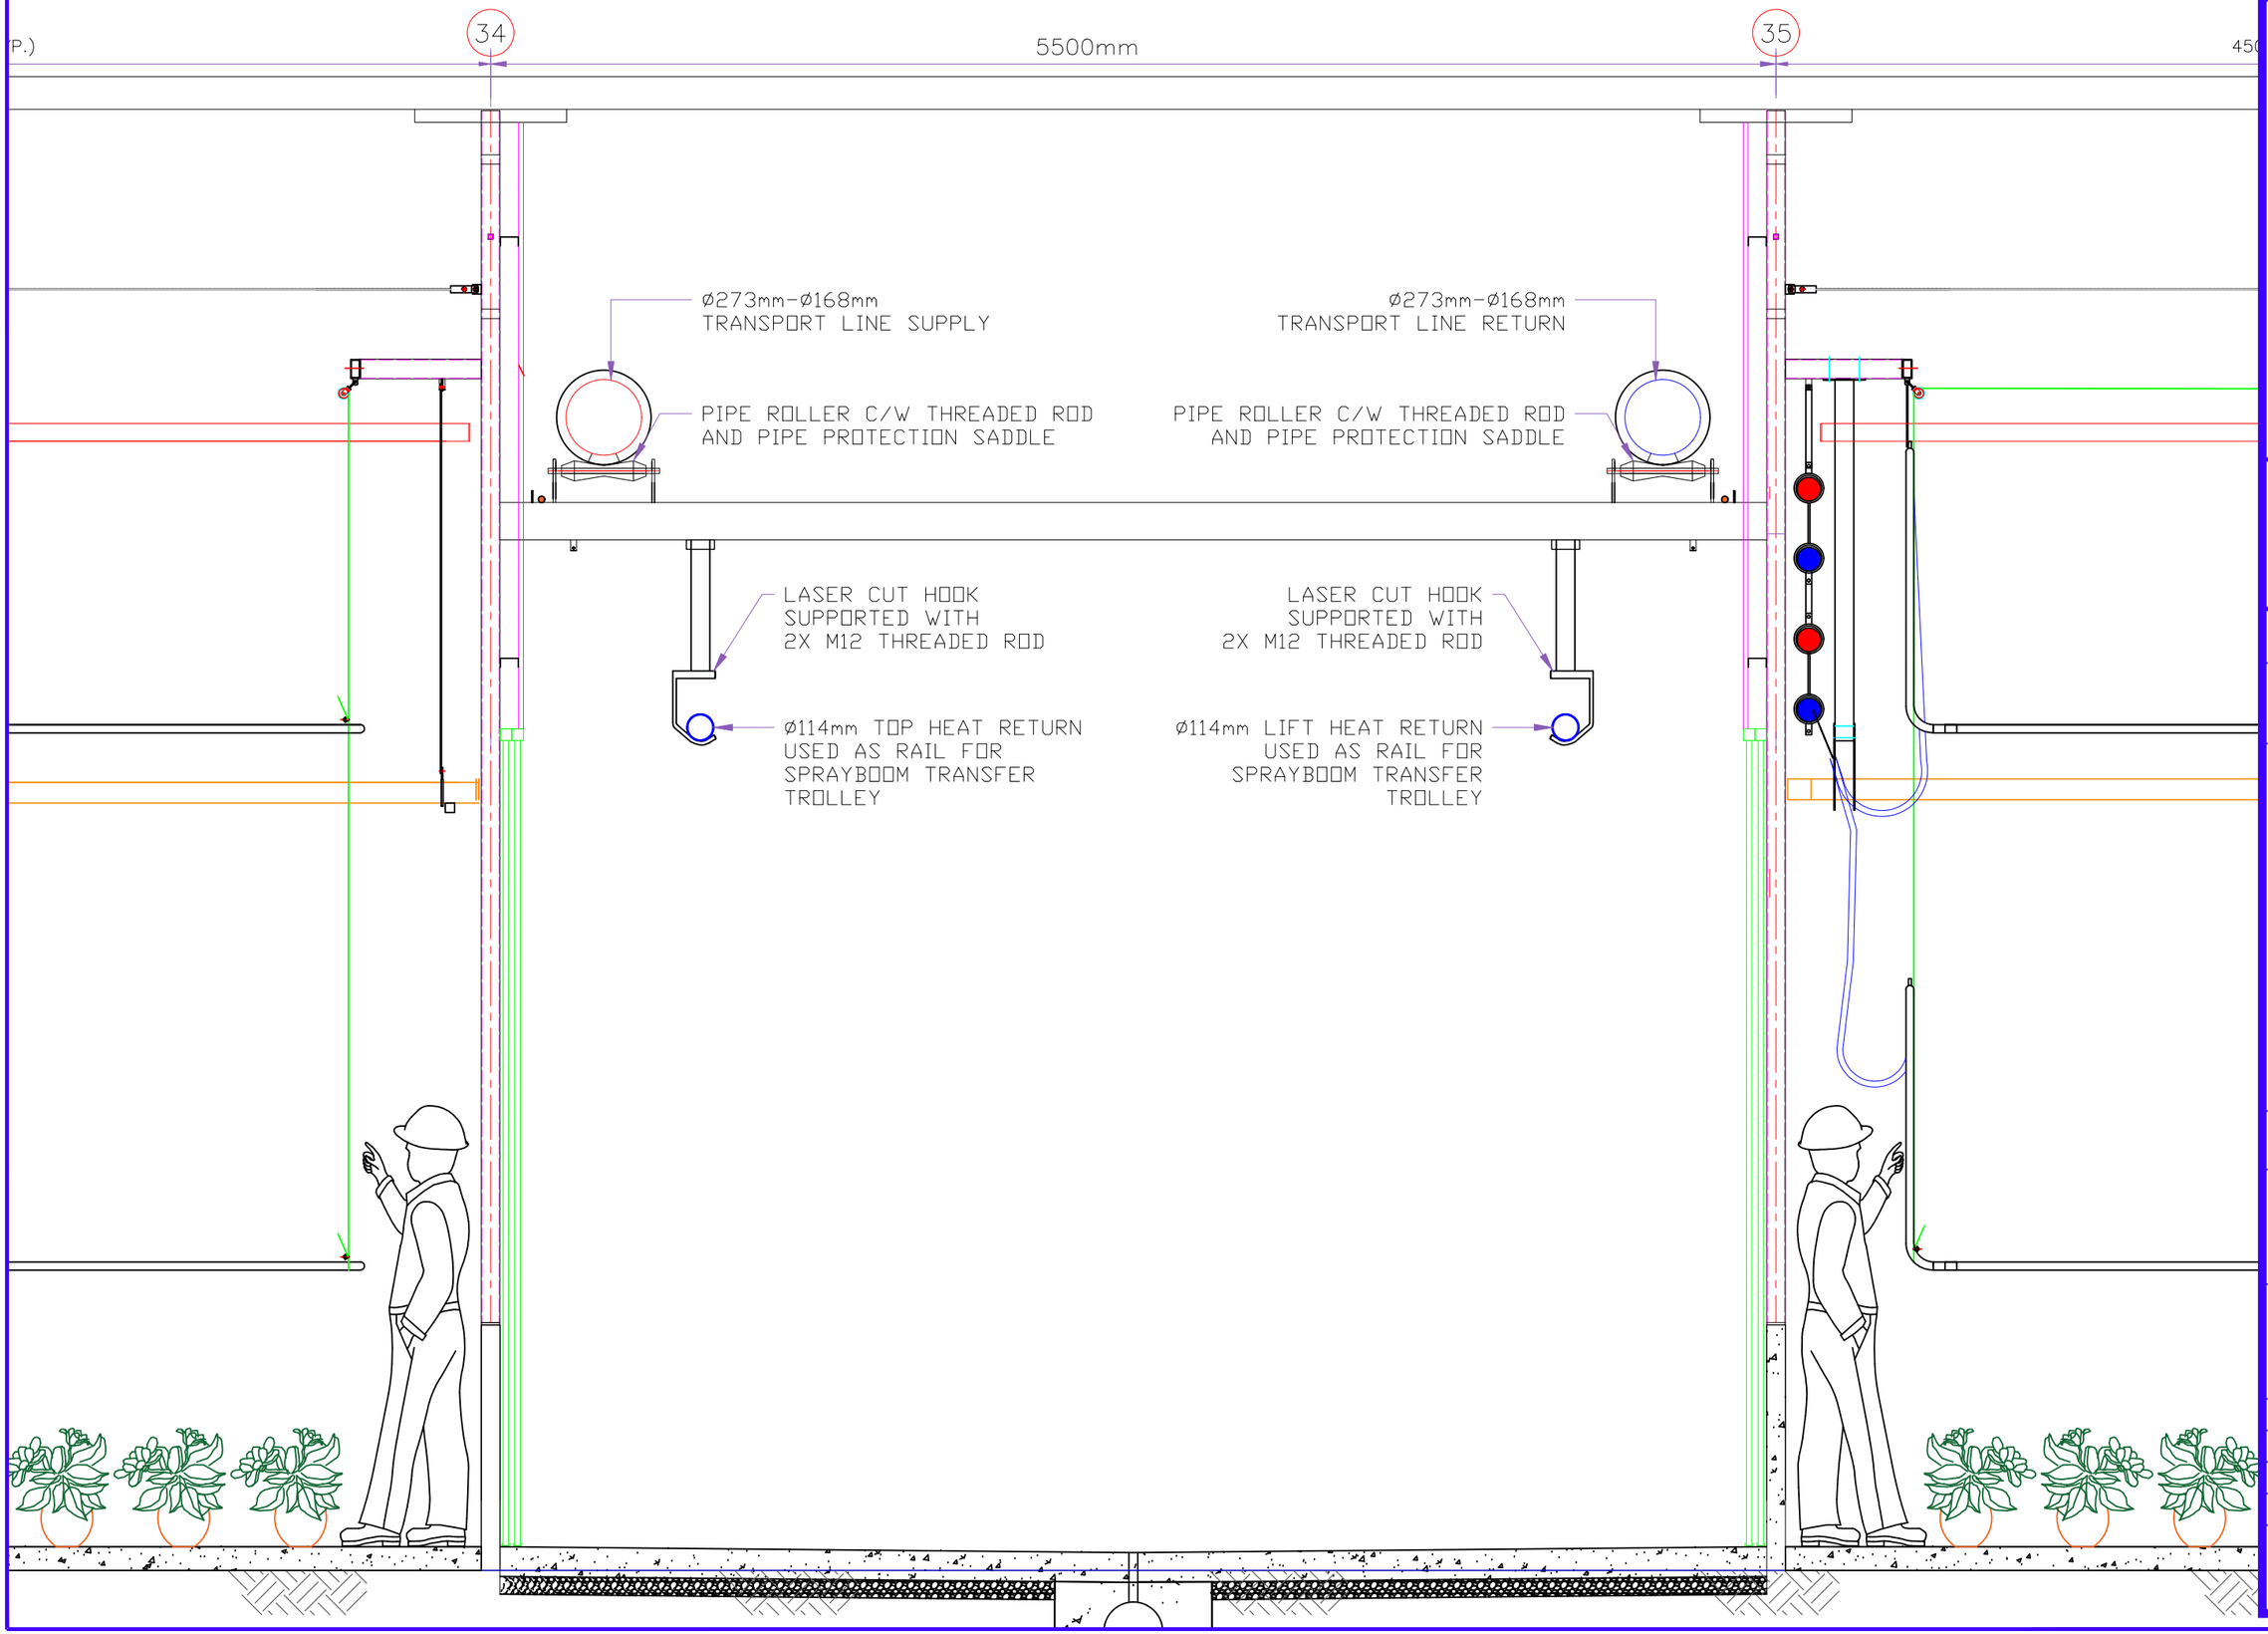

PRINS
Greenhouses
38900 NO.4 ROAD
ABBOTSFORD B.C
CANADA V3G 2G2
TEL (604) 852-4001
FAX (604) 852-4090

ALL DRAWINGS AND RELATED DOCUMENTS ARE THE COPYRIGHT OF PRINS GREENHOUSES LIMITED AND MUST BE RETURNED UPON REQUEST. REPRODUCTIONS IN PART OR WHOLE ARE FORBIDDEN WITHOUT WRITTEN PERMISSION.

REV	ACTION	DATE	BY

CUSTOMER
SCHENCK FARMS

TITLE
WALKWAY CROSS SECTION AT GL34/35

DATE: FEB 23, 2024
DRAWN: MR
CHECKED: MR
PROJECT: 24-4591

SHEET No.	REV.
HE-010	-

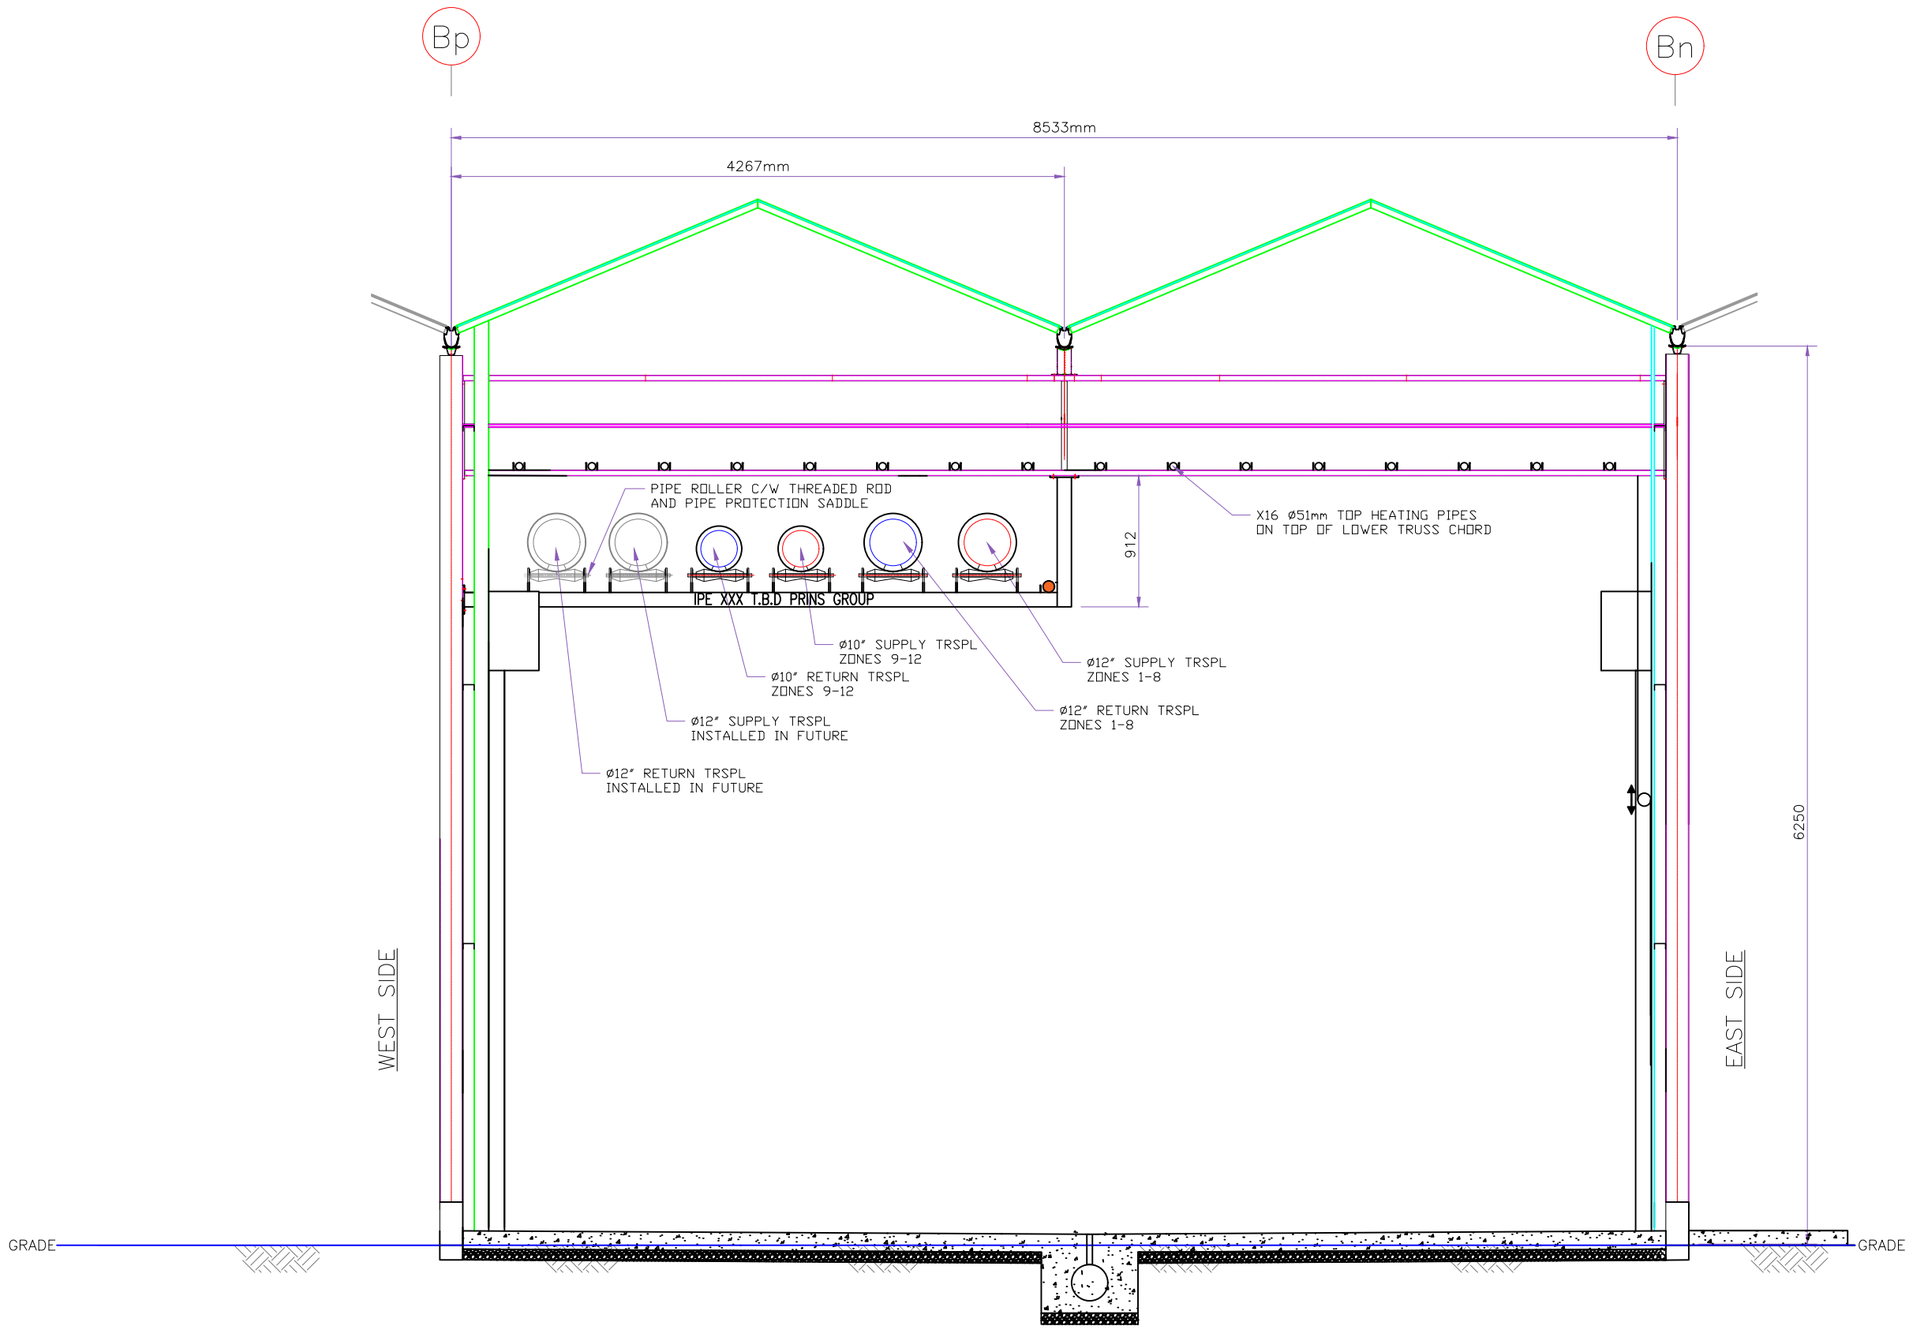

PRINS
Greenhouses
38900 NO.4 ROAD
ABBOTSFORD B.C
CANADA V3G 2G2
TEL (604) 852-4001
FAX (604) 852-4090
3500 SOUTH SERVICE RD.
VINELAND STATION, ON.
CANADA L0R 2E0
TEL (905) 562-4411
FAX (905) 562-5533

ALL DRAWINGS AND RELATED DOCUMENTS ARE THE COPYRIGHT OF PRINS GREENHOUSES LIMITED AND MUST BE RETURNED UPON REQUEST. REPRODUCTIONS IN PART OR WHOLE ARE FORBIDDEN WITHOUT WRITTEN PERMISSION.

REV	ACTION	DATE	BY
A	FUTURE LINES INDICATED	06/13/25	DM

CUSTOMER
SCHENCK FARMS

TITLE
WEST CORRIDOR
CROSS SECTION
GLII-17

DATE: June 9, 2025
DRAWN: DM
CHECKED: MR
PROJECT: 24-4591

SHEET No.	REV.
HE-013	A

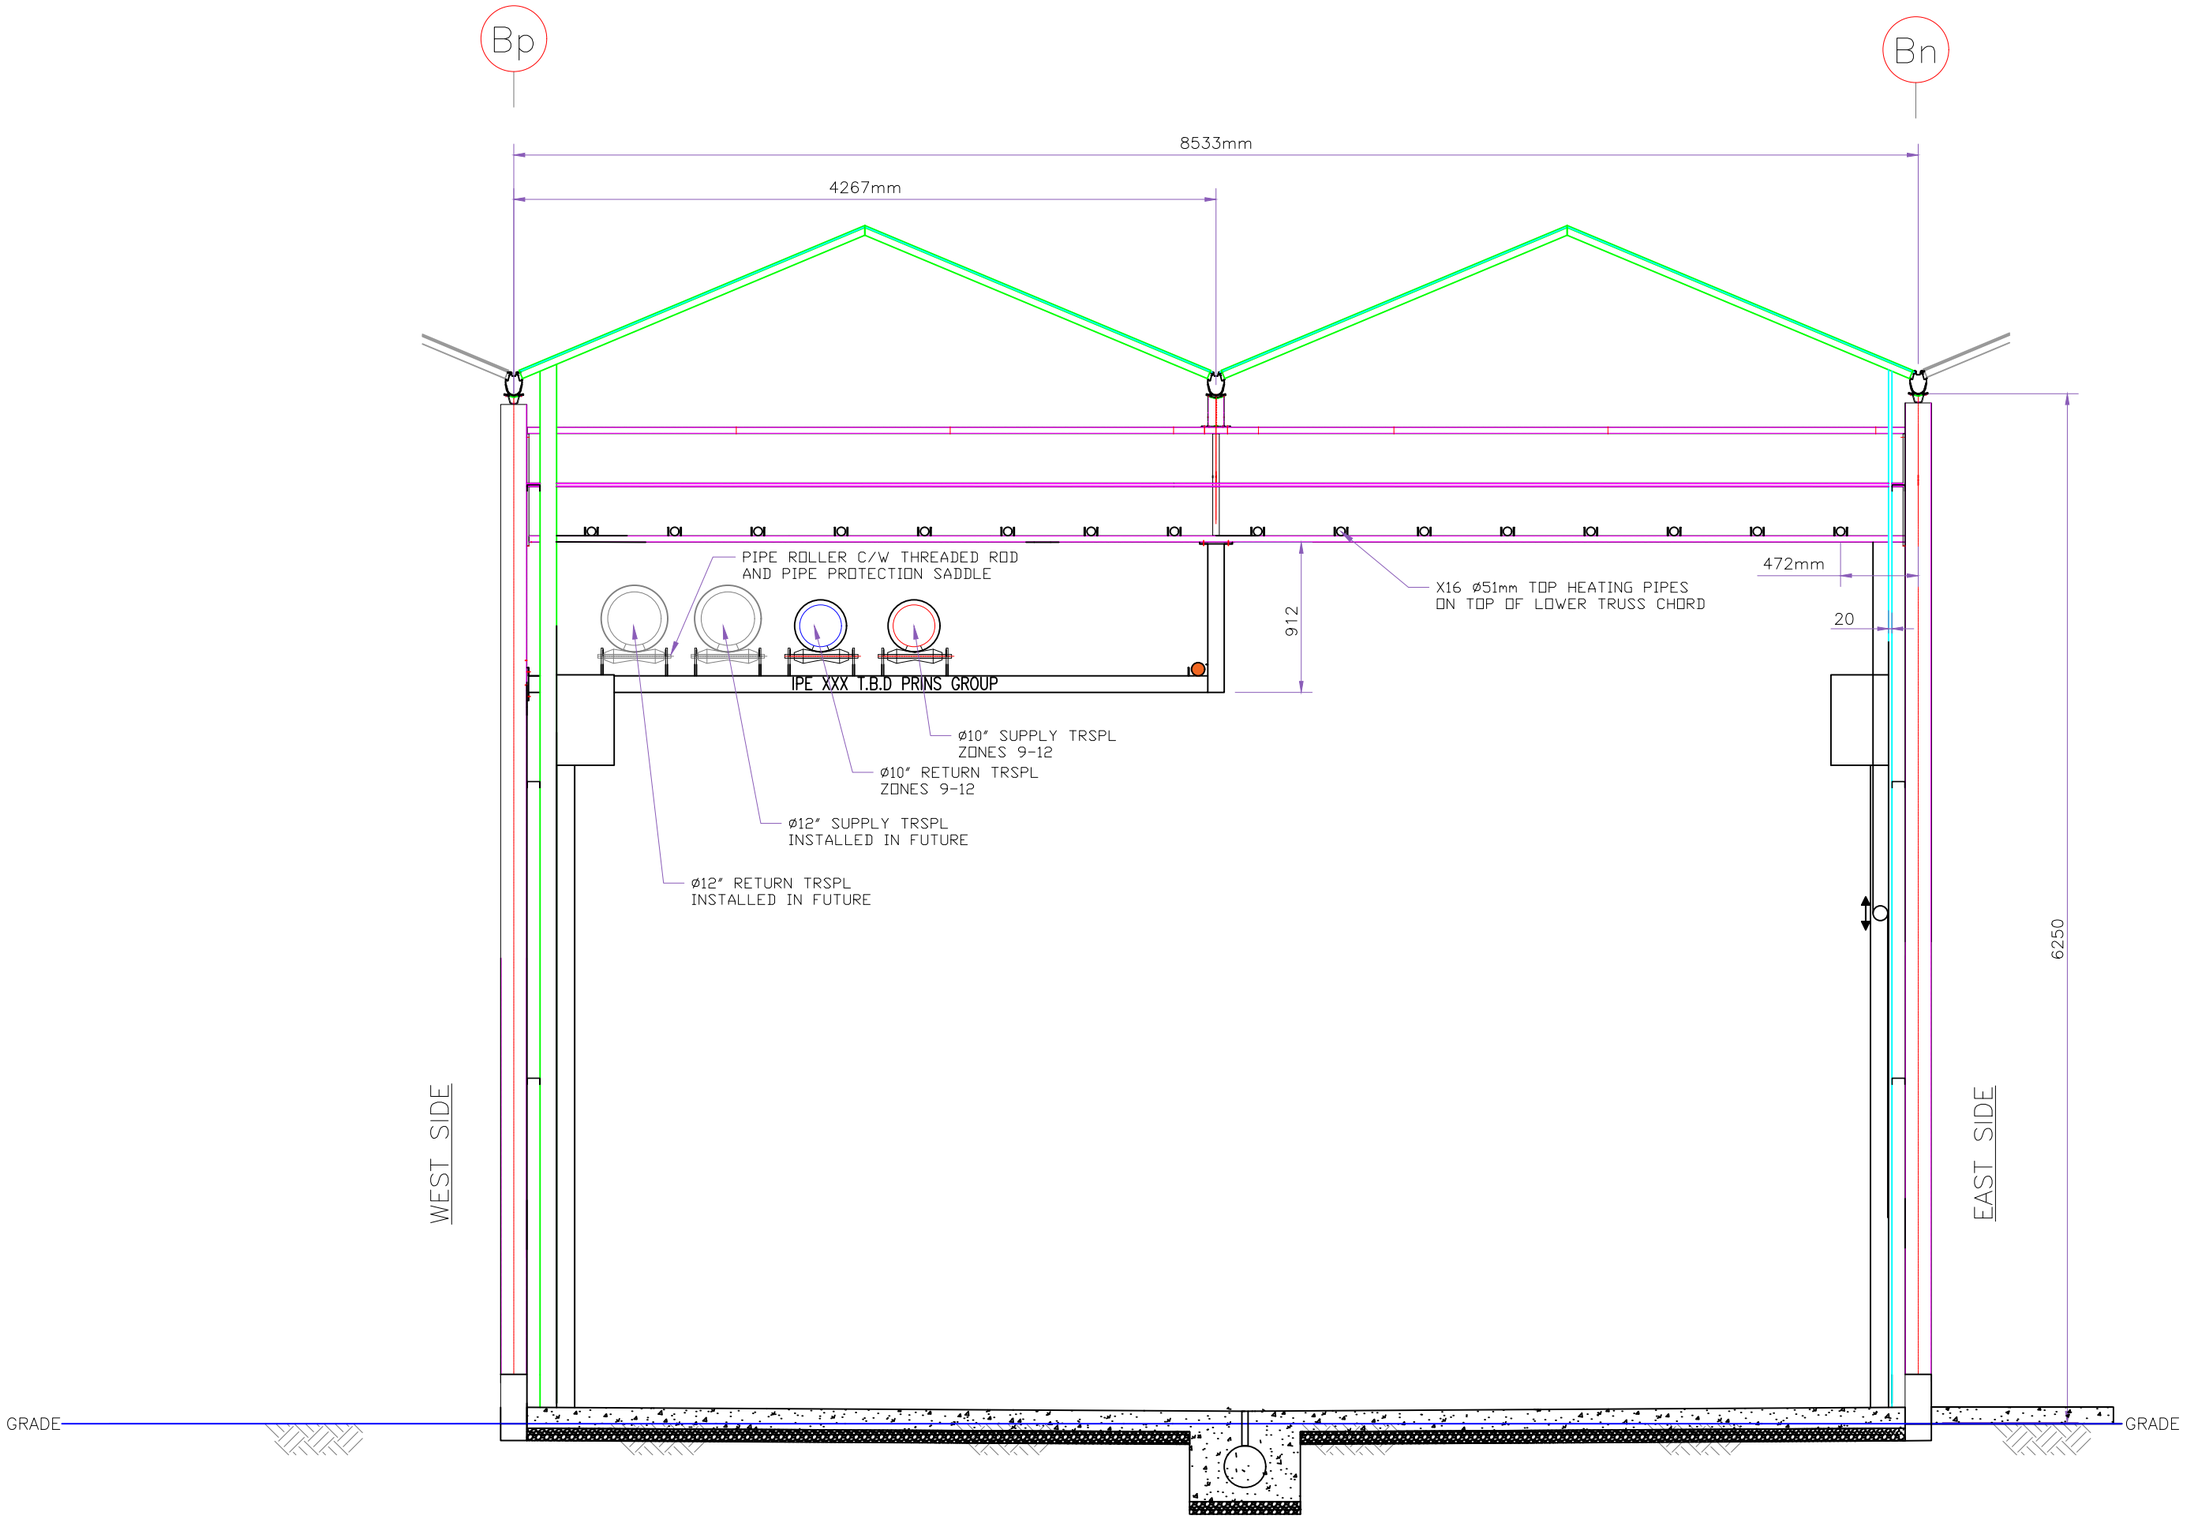

PRINS
Greenhouses
38900 NO.4 ROAD
ABBOTSFORD B.C
CANADA V3G 2G2
TEL (604) 852-4001
FAX (604) 852-4090
3500 SOUTH SERVICE RD.
VINELAND STATION, ON.
CANADA L0R 2E0
TEL (905) 562-4411
FAX (905) 562-5533

ALL DRAWINGS AND RELATED DOCUMENTS ARE THE COPYRIGHT OF PRINS GREENHOUSES LIMITED AND MUST BE RETURNED UPON REQUEST. REPRODUCTIONS IN PART OR WHOLE ARE FORBIDDEN WITHOUT WRITTEN PERMISSION.

REV	ACTION	DATE	BY
A	FUTURE LINES INDICATED	06/13/25	DM

CUSTOMER
SCHENCK FARMS

TITLE
WEST CORRIDOR
CROSS SECTION GL
18-34

DATE: June 9, 2025
DRAWN: DM
CHECKED: MR
PROJECT: 24-4591

SHEET No.	REV.
HE-014	A

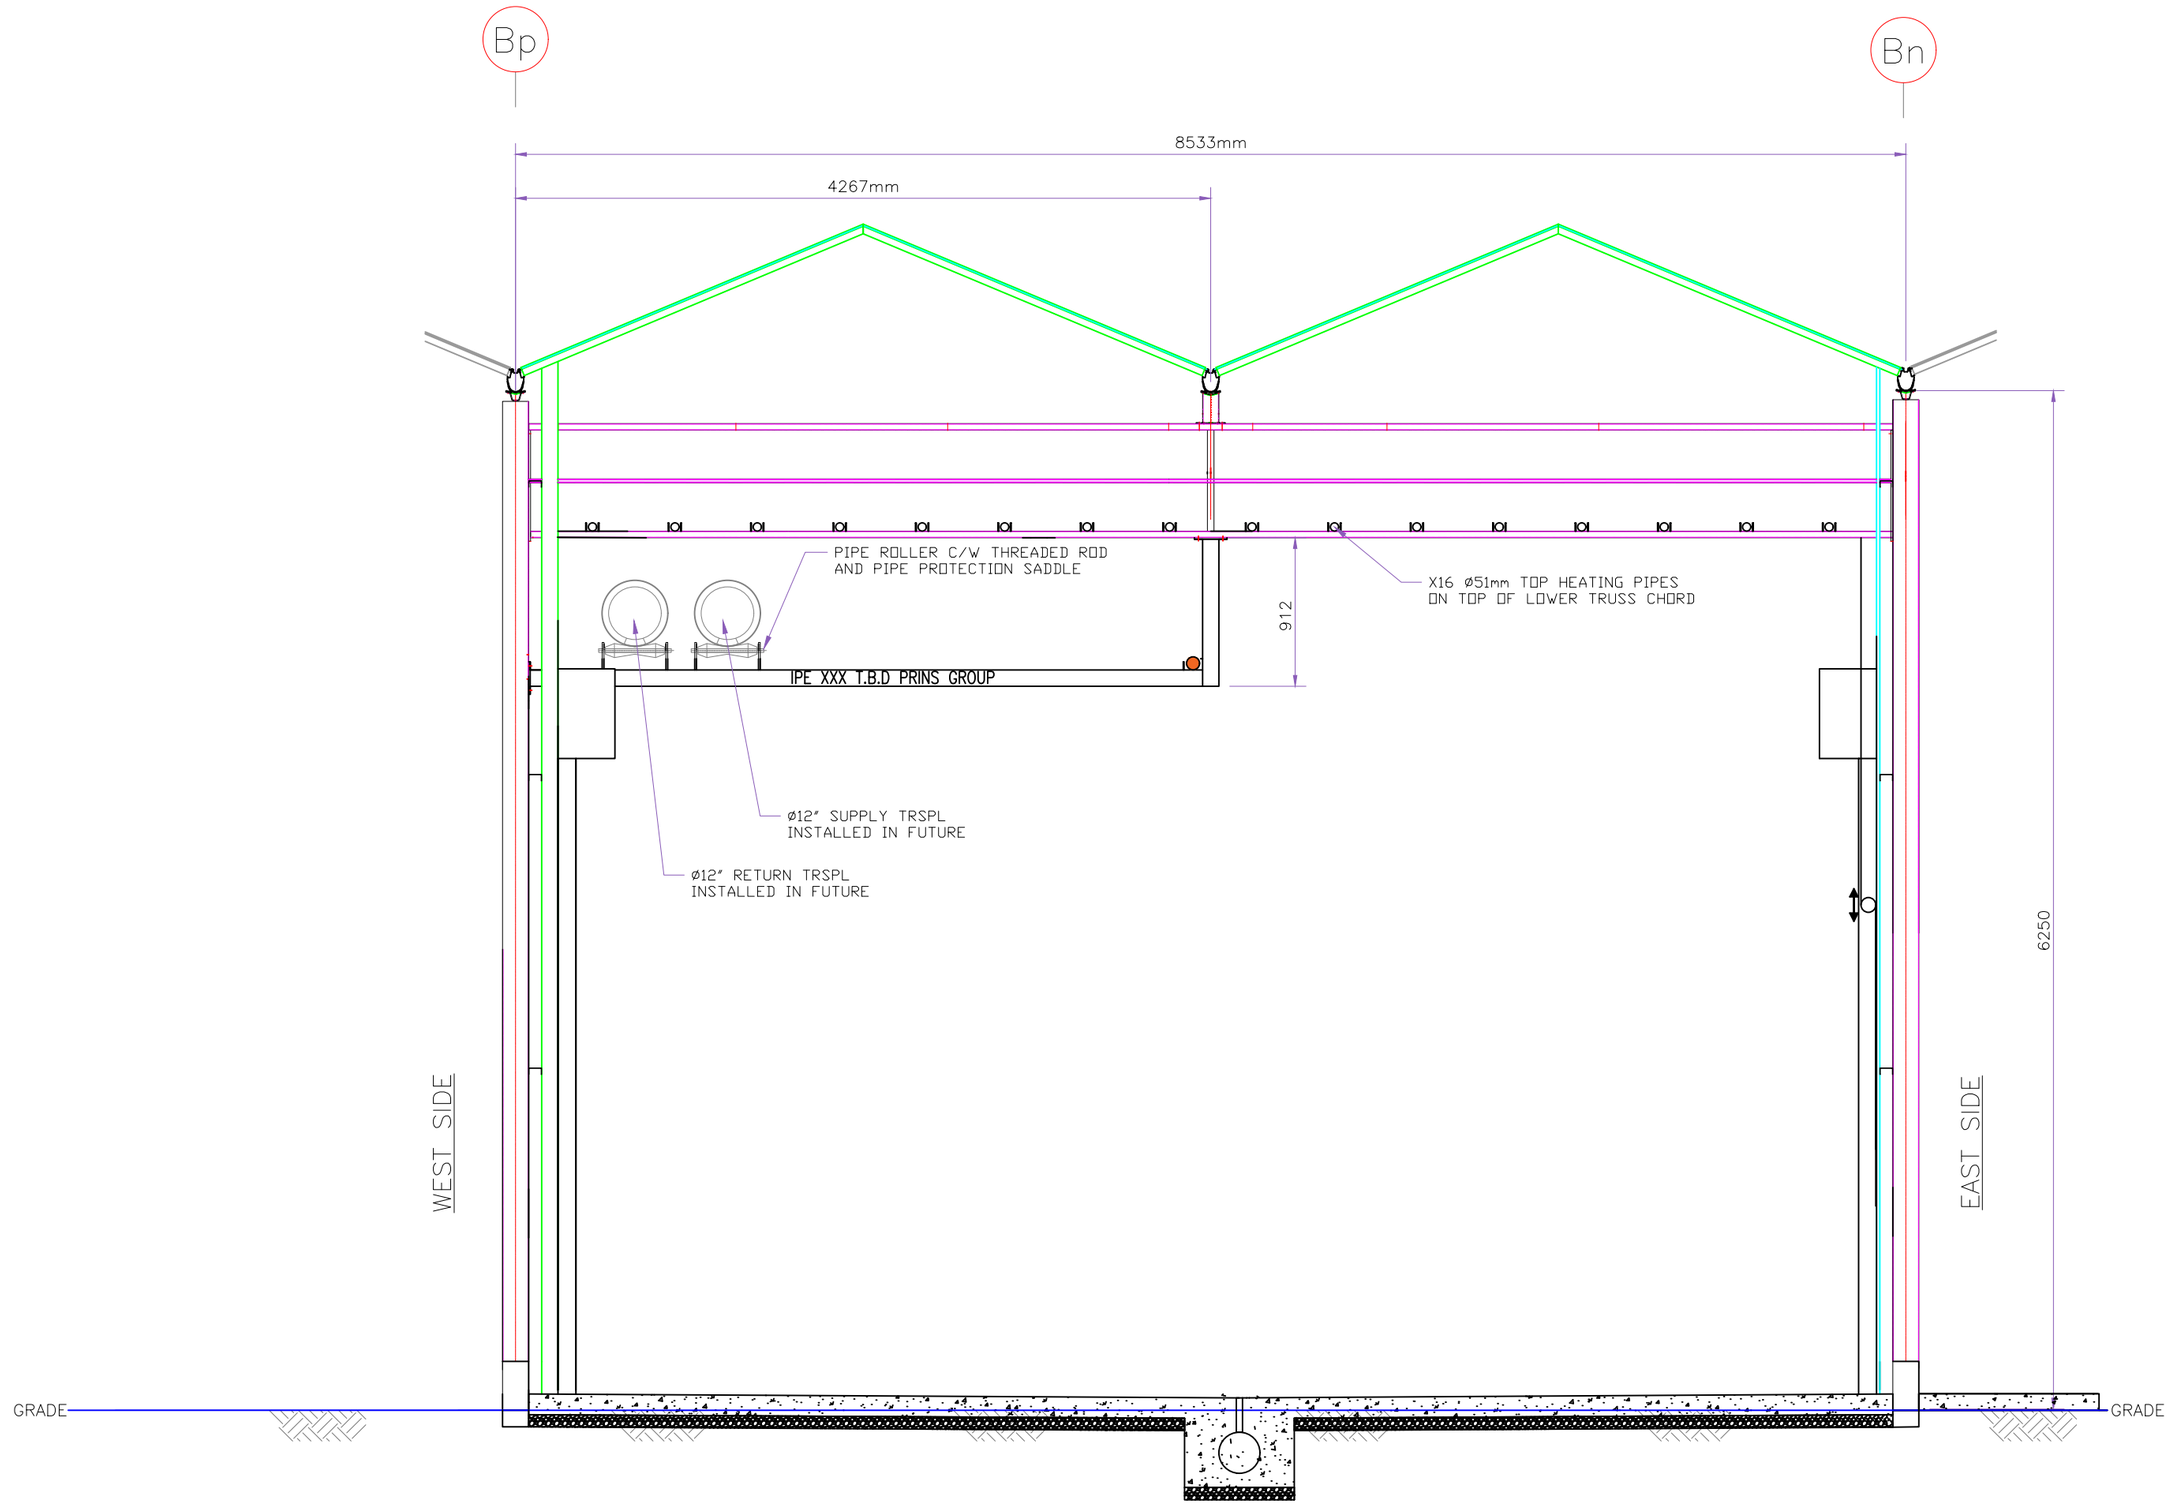

PRINS
Greenhouses

38900 NO.4 ROAD
ABBOTSFORD B.C
CANADA V3G 2G2
TEL (604) 852-4001
FAX (604) 852-4090

3500 SOUTH SERVICE RD.
VINELAND STATION, ON.
CANADA L0R 2E0
TEL (905) 562-4411
FAX (905) 562-5533

ALL DRAWINGS AND RELATED DOCUMENTS ARE THE COPYRIGHT OF PRINS GREENHOUSES LIMITED AND MUST BE RETURNED UPON REQUEST. REPRODUCTIONS IN PART OR WHOLE ARE FORBIDDEN WITHOUT WRITTEN PERMISSION.

REV	ACTION	DATE	BY
A	FUTURE LINES INDCIATED	06/13/25	DM

CUSTOMER
SCHENCK FARMS

TITLE
WEST CORRIDOR
CROSS SECTION GL
35-51

DATE: June 9, 2025
DRAWN: DM
CHECKED: MR
PROJECT: 24-4591

SHEET No.	REV.
HE-015	A